


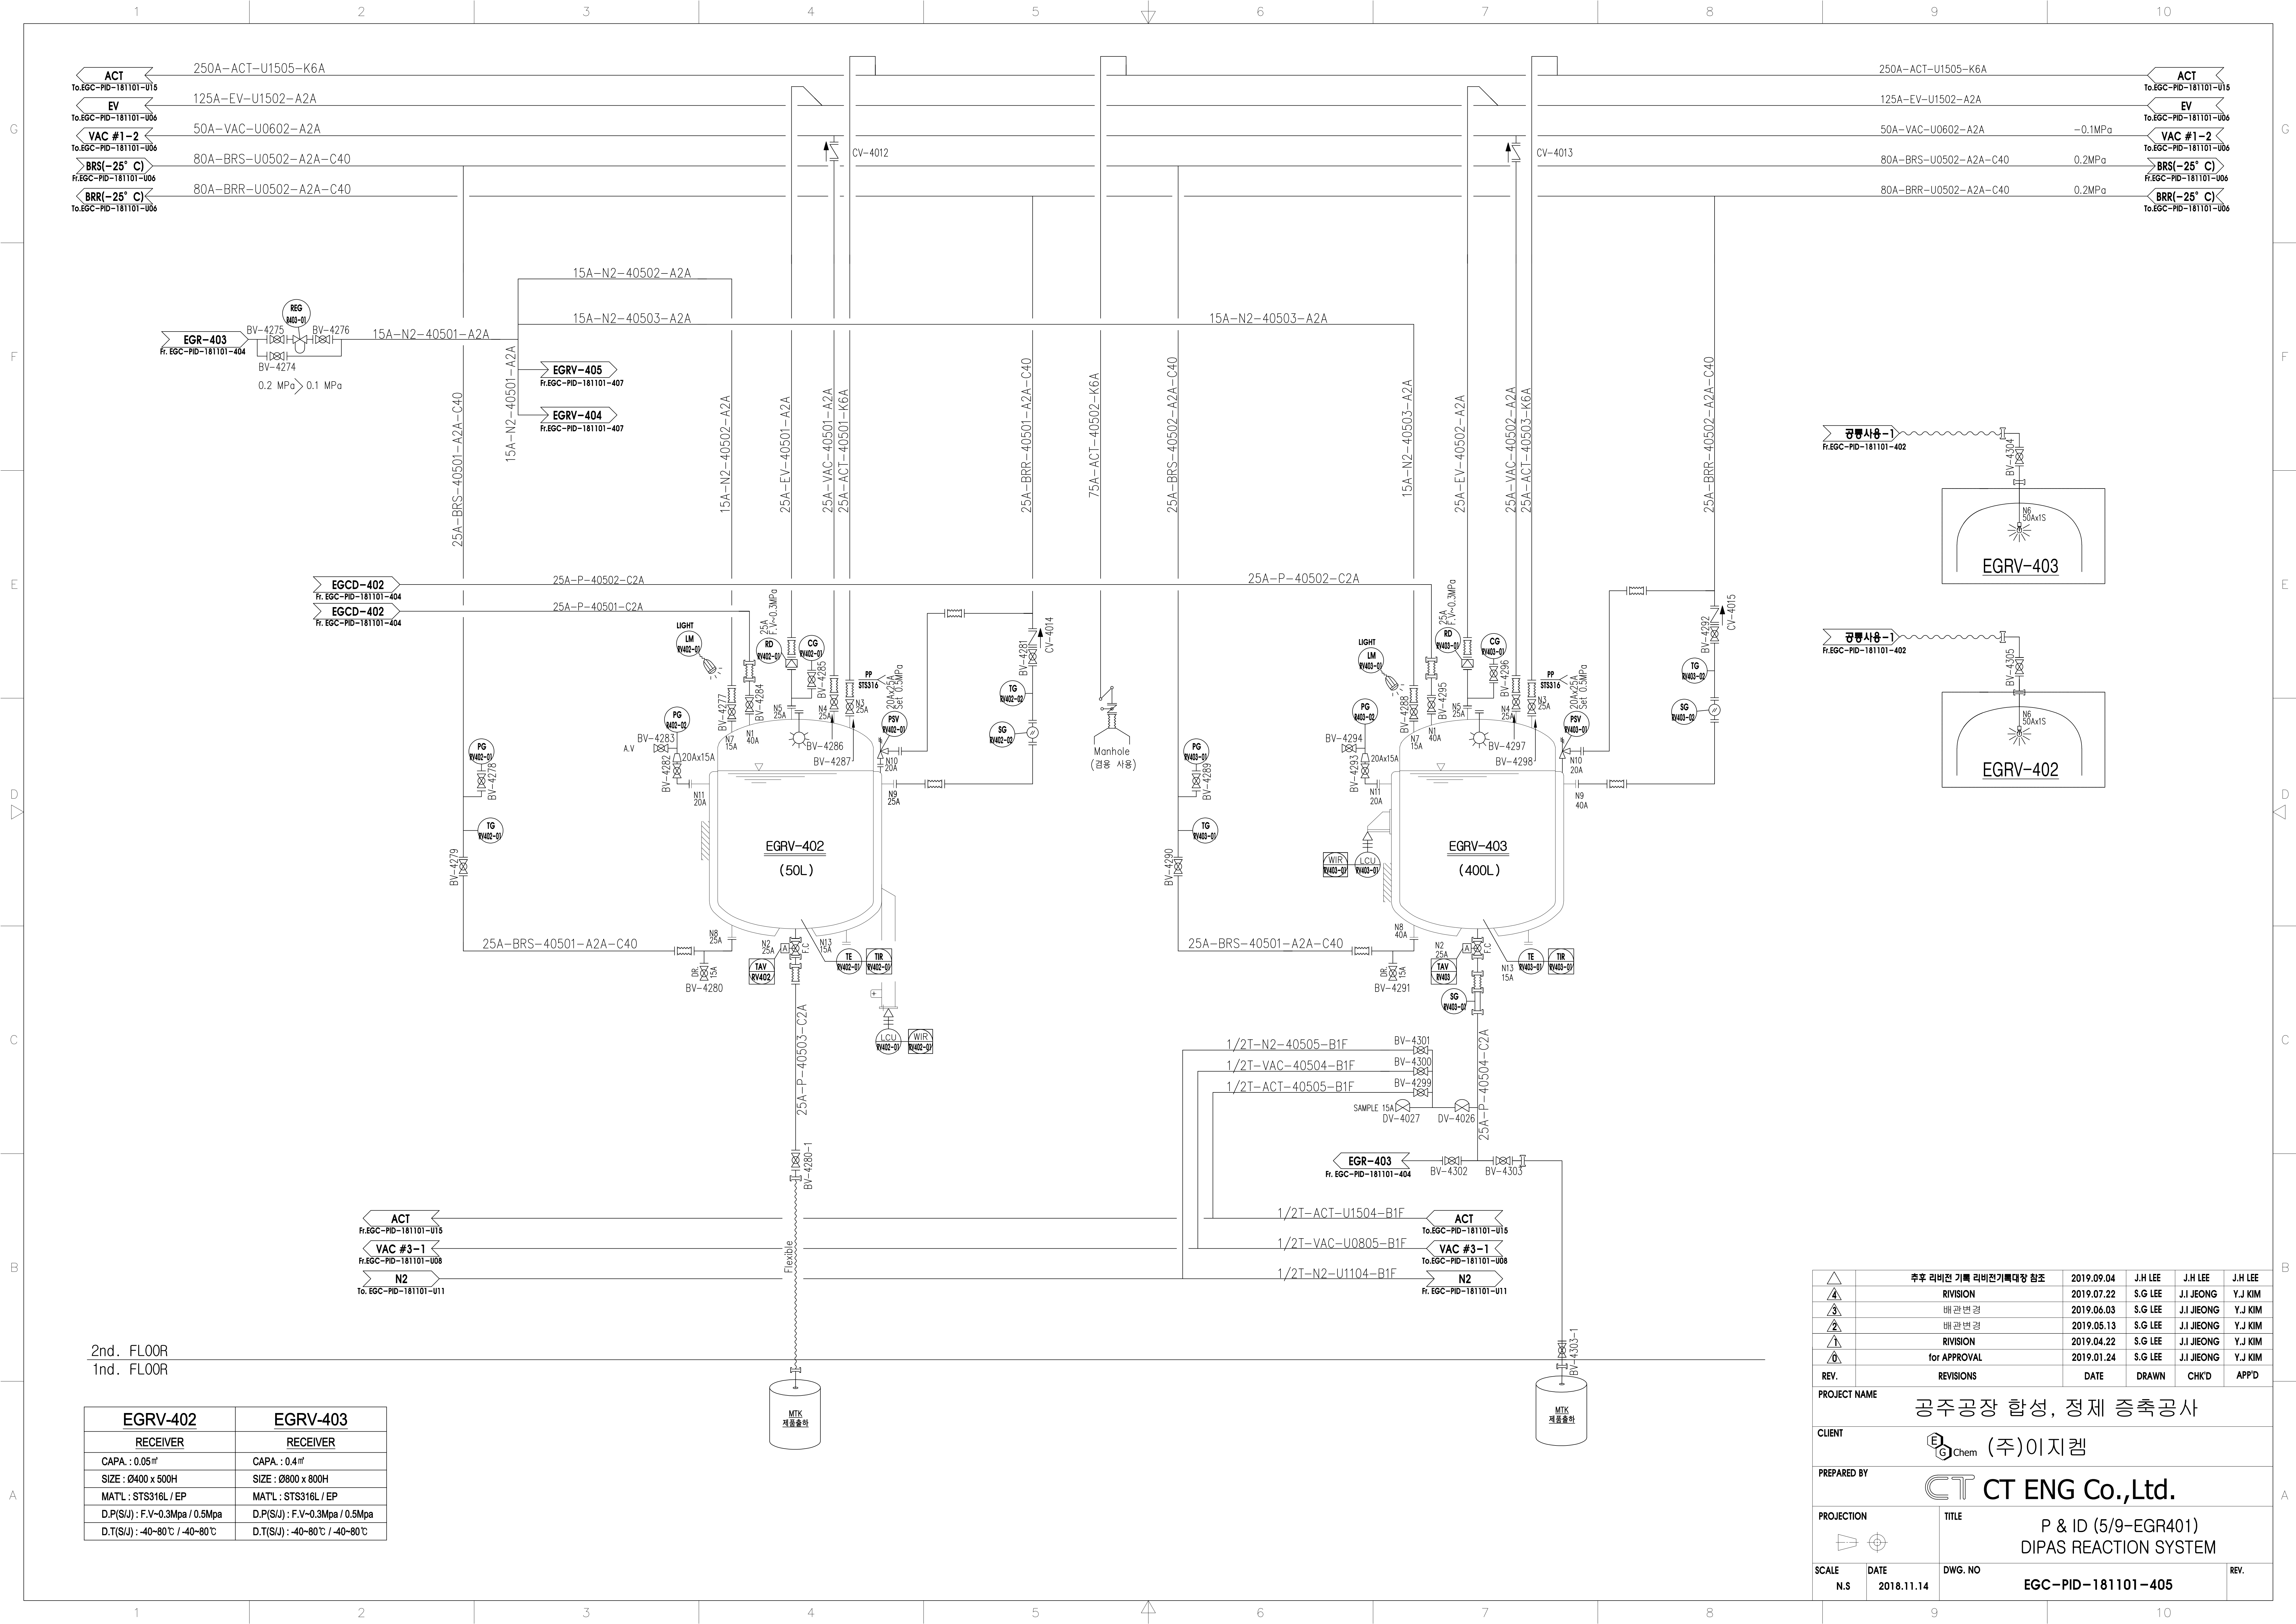

2nd. FLOOR
1nd. FLOOR

EGRV-402	EGRV-403
RECEIVER	RECEIVER
CAPA : 0.05㎡	CAPA : 0.4㎡
SIZE : Ø400 x 500H	SIZE : Ø800 x 800H
MAT'L : STS316L / EP	MAT'L : STS316L / EP
D.P(S/U) : F.V-0.3Mpa / 0.5Mpa	D.P(S/U) : F.V-0.3Mpa / 0.5Mpa
D.T(S/U) : -40~80℃ / -40~80℃	D.T(S/U) : -40~80℃ / -40~80℃

△	추후 리비전 기록 리비전기록대장 참조	2019.09.04	J.H LEE	J.H LEE	J.H LEE
④	RIVISION	2019.07.22	S.G LEE	J.I JEONG	Y.J KIM
③	배관변경	2019.06.03	S.G LEE	J.I JEONG	Y.J KIM
②	배관변경	2019.06.13	S.G LEE	J.I JEONG	Y.J KIM
①	RIVISION	2019.04.22	S.G LEE	J.I JEONG	Y.J KIM
①	for APPROVAL	2019.01.24	S.G LEE	J.I JEONG	Y.J KIM
REV.	REVISIONS	DATE	DRAWN	CHK'D	APP'D

PROJECT NAME 공주공장 합성, 정제 증축공사					
CLIENT Chem (주)이지캠					
PREPARED BY CT CT ENG Co.,Ltd.					
PROJECTION P & ID		TITLE P & ID (5/9-EGR401) DIPAS REACTION SYSTEM			
SCALE N.S	DATE 2018.11.14	DWG. NO EGC-PID-181101-405	REV.		