


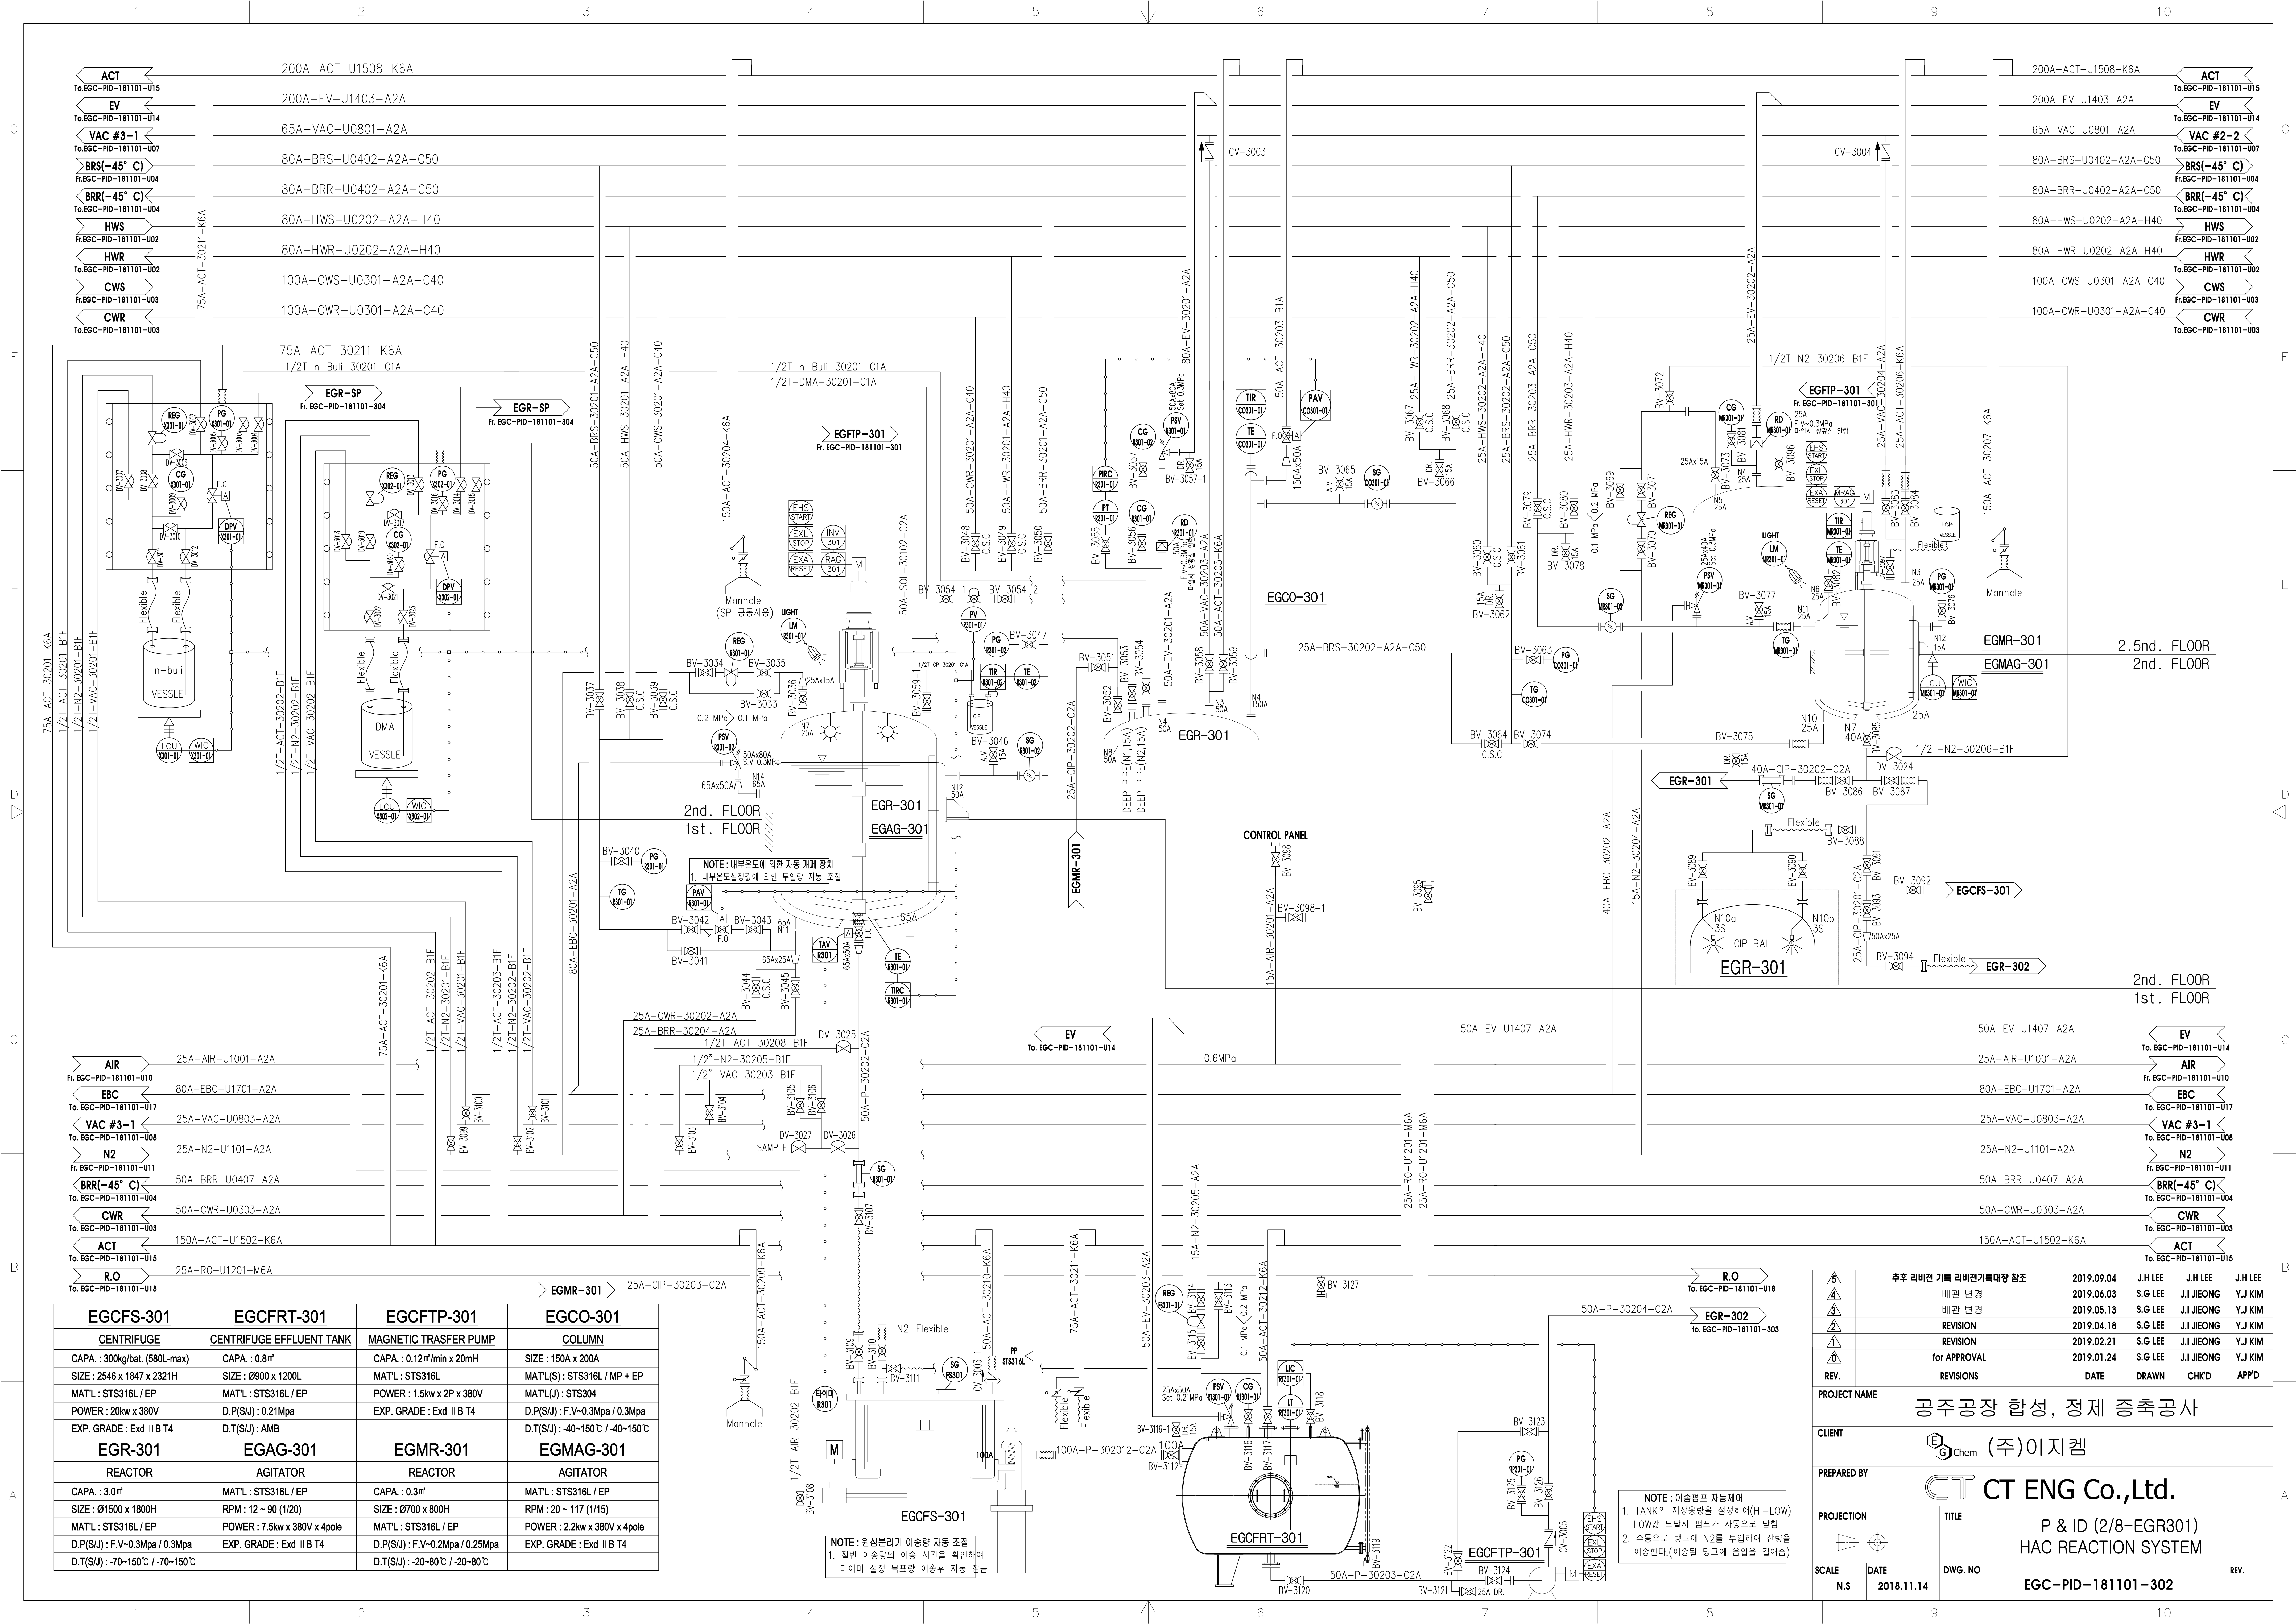

EGCFS-301	EGCFRT-301	EGCFTP-301	EGCO-301
CENTRIFUGE	CENTRIFUGE EFFLUENT TANK	MAGNETIC TRASFER PUMP	COLUMN
CAPA : 300kg/bat. (580L-max)	CAPA : 0.8m³	CAPA : 0.12m³/min x 20mH	SIZE : 150A x 200A
SIZE : 2546 x 1847 x 2321H	SIZE : Ø900 x 1200L	MAT'L : STS316L	MAT'L(S) : STS316L / MP + EP
MAT'L : STS316L / EP	MAT'L : STS316L / EP	POWER : 1.5kw x 2P x 380V	MAT'L(U) : STS304
POWER : 20kw x 380V	D.P(S/U) : 0.21Mpa	EXP. GRADE : Exd IIB T4	D.P(S/U) : F.V-0.3Mpa / 0.3Mpa
EXP. GRADE : Exd IIB T4	D.T(S/U) : AMB		D.T(S/U) : 40~150℃ / 40~150℃
EGR-301	EGAG-301	EGMR-301	EGMAG-301
REACTOR	AGITATOR	REACTOR	AGITATOR
CAPA : 3.0m³	MAT'L : STS316L / EP	CAPA : 0.3m³	MAT'L : STS316L / EP
SIZE : Ø1500 x 1800H	RPM : 12 ~ 90 (1/20)	SIZE : Ø700 x 800H	RPM : 20 ~ 117 (1/15)
MAT'L : STS316L / EP	POWER : 7.5kw x 380V x 4pole	MAT'L : STS316L / EP	POWER : 2.2kw x 380V x 4pole
D.P(S/U) : F.V-0.3Mpa / 0.3Mpa	EXP. GRADE : Exd IIB T4	D.P(S/U) : F.V-0.2Mpa / 0.25Mpa	EXP. GRADE : Exd IIB T4
D.T(S/U) : -70~150℃ / -70~150℃		D.T(S/U) : -20~80℃ / -20~80℃	

주요 리비전 기록	리비전기	2019.09.04	J.H LEE	J.H LEE	J.H LEE
배관 변경		2019.06.03	S.G LEE	J.I JEONG	Y.J KIM
배관 변경		2019.05.13	S.G LEE	J.I JEONG	Y.J KIM
REVISION		2019.04.18	S.G LEE	J.I JEONG	Y.J KIM
REVISION		2019.02.21	S.G LEE	J.I JEONG	Y.J KIM
for APPROVAL		2019.01.24	S.G LEE	J.I JEONG	Y.J KIM
REV.	REVISIONS	DATE	DRAWN	CHK'D	APP'D
PROJECT NAME 공주공장 합성, 정제 증축공사					
CLIENT CT Chem (주)이지캠					
PREPARED BY CT CT ENG Co.,Ltd.					
PROJECTION	TITLE P & ID (2/8-EGR301) HAC REACTION SYSTEM				
SCALE N.S	DATE 2018.11.14	DWG. NO EGC-PID-181101-302	REV.		