


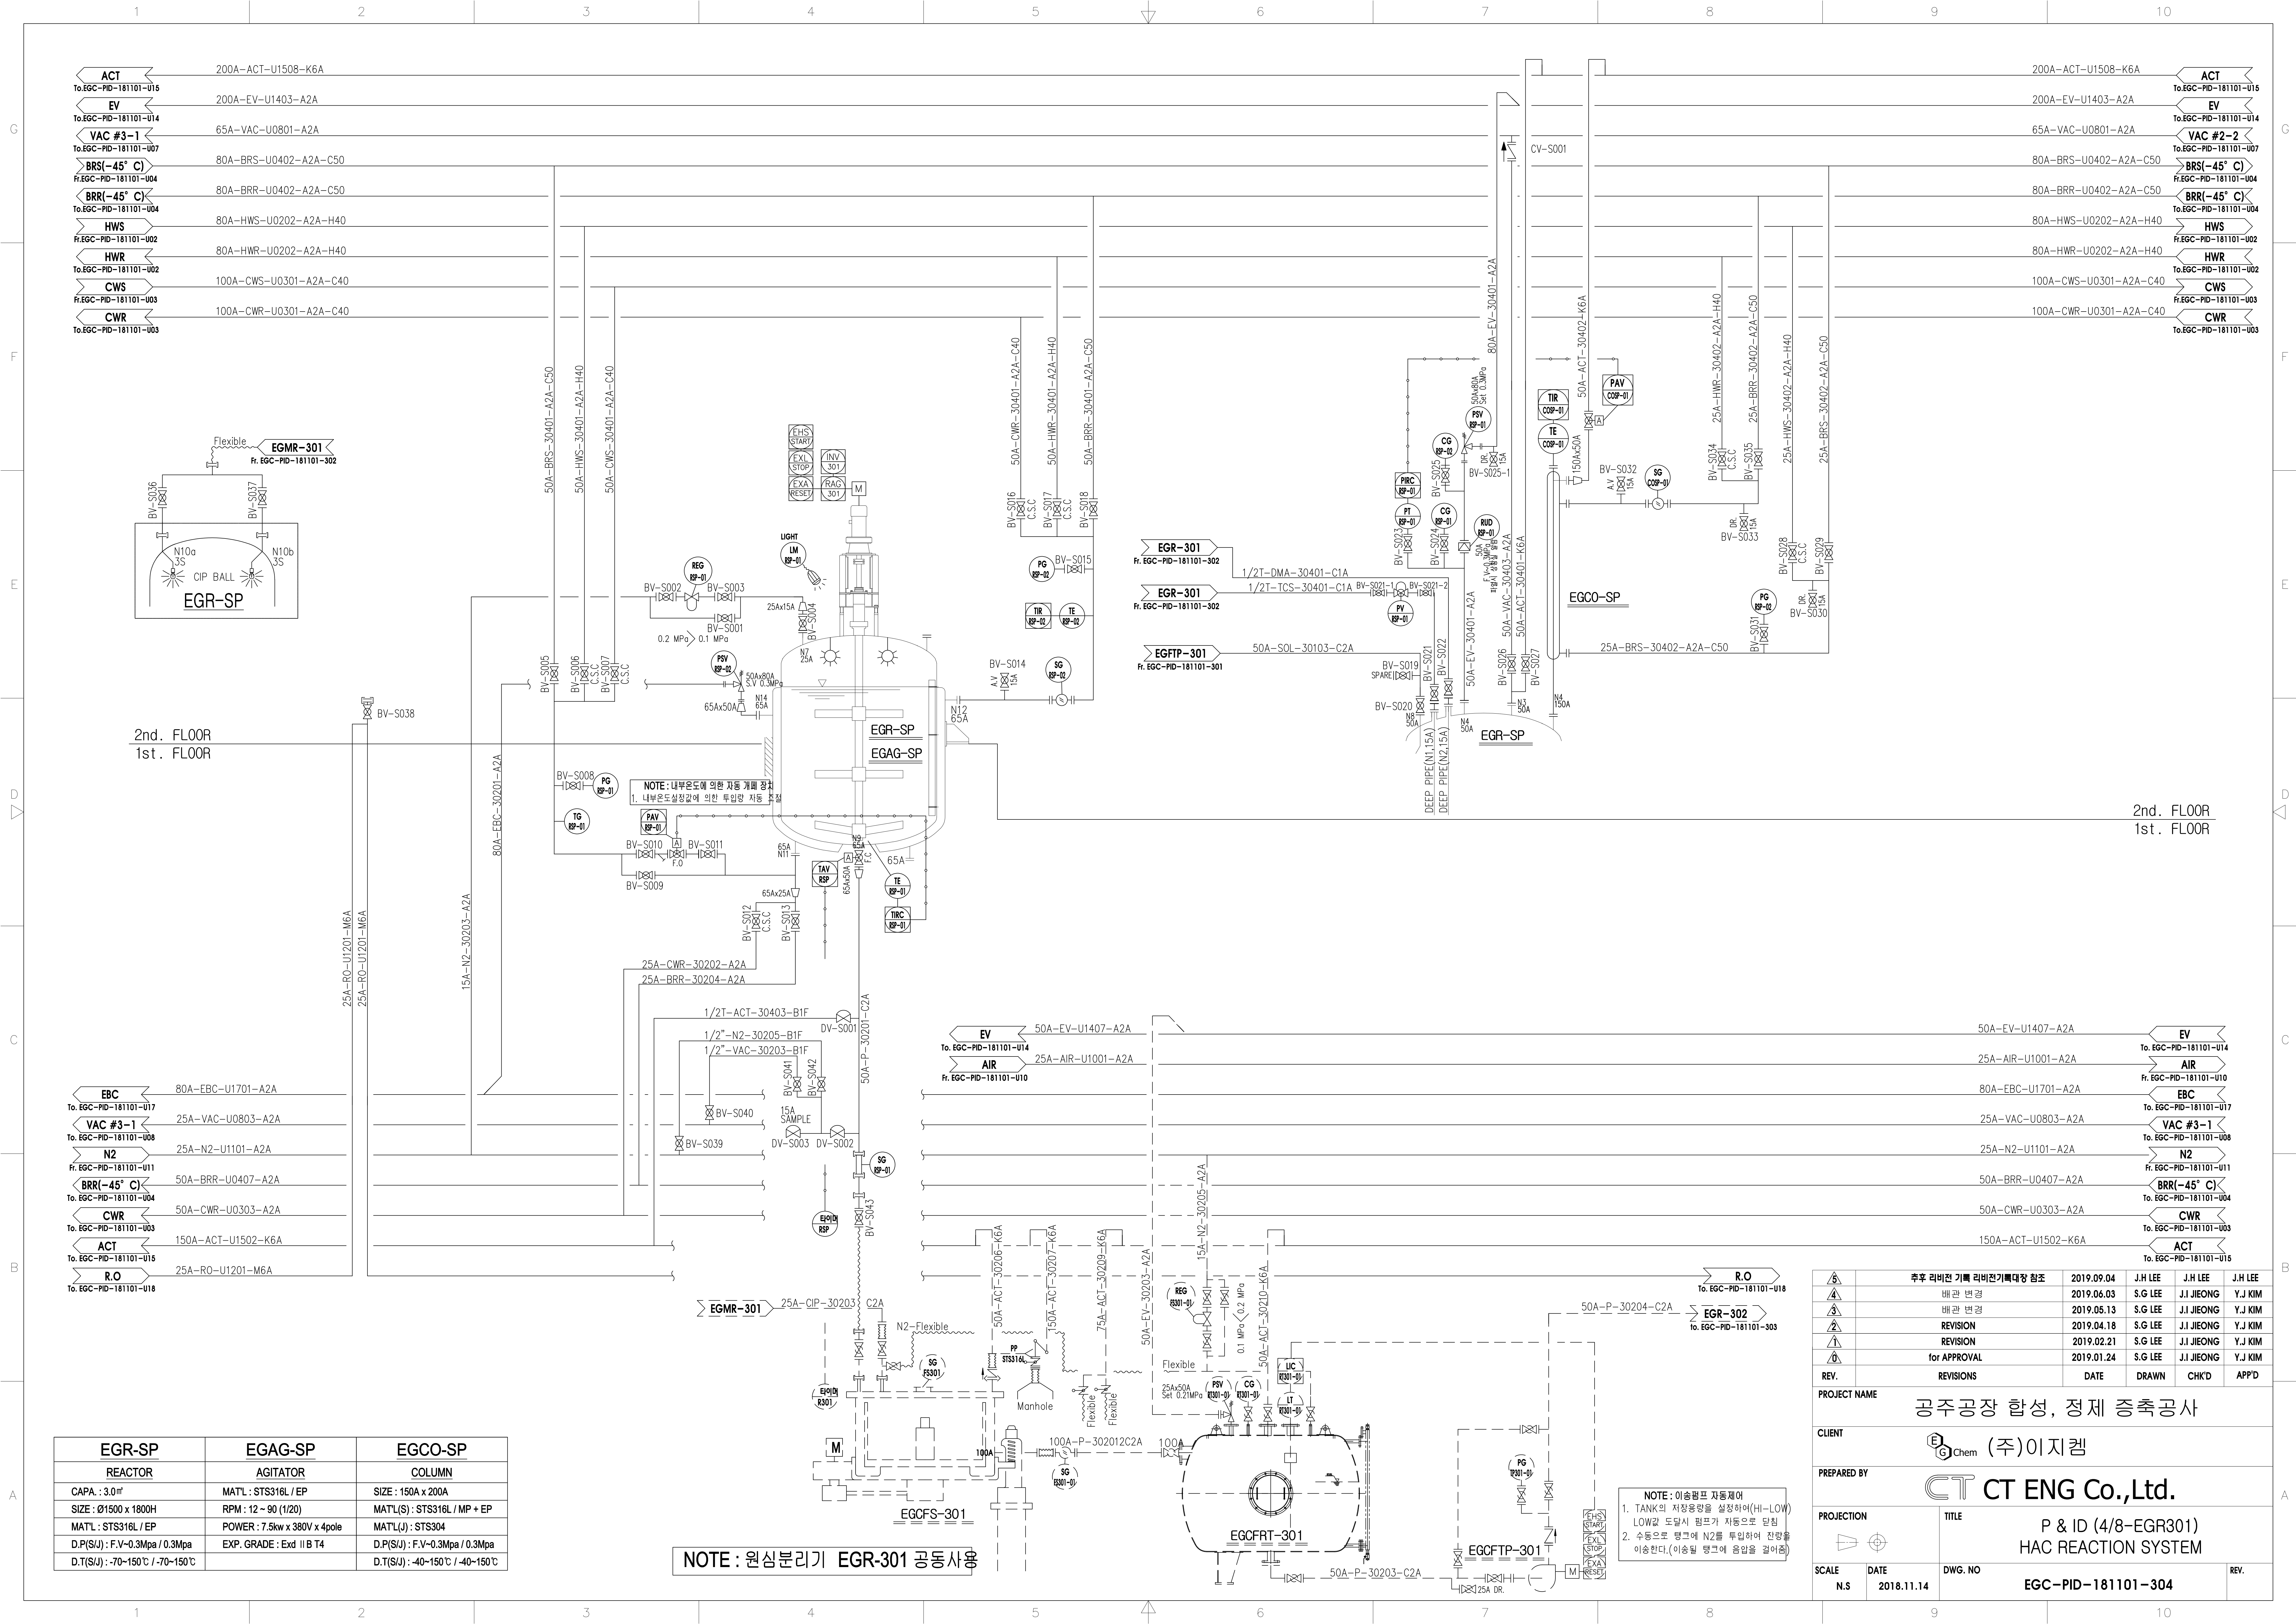

EBC	80A-EBC-U1701-A2A
To: EGC-PID-181101-U17	
VAC #3-1	25A-VAC-U0803-A2A
To: EGC-PID-181101-U08	
N2	25A-N2-U1101-A2A
Fr: EGC-PID-181101-U11	
BRR(-45° C)	50A-BRR-U0407-A2A
To: EGC-PID-181101-U04	
CWR	50A-CWR-U0303-A2A
To: EGC-PID-181101-U03	
ACT	150A-ACT-U1502-K6A
To: EGC-PID-181101-U15	
R.O	25A-RQ-U1201-M6A
To: EGC-PID-181101-U18	

EGR-SP	EGAG-SP	EGCO-SP
REACTOR	AGITATOR	COLUMN
CAPA : 3.0m ³	MAT'L : STS316L / EP	SIZE : 150A x 200A
SIZE : Ø1500 x 1800H	RPM : 12 ~ 90 (1/20)	MAT'L(S) : STS316L / MP + EP
MAT'L : STS316L / EP	POWER : 7.5kw x 380V x 4pole	MAT'L(J) : STS304
D.P(S/U) : F.V-0.3Mpa / 0.3Mpa	EXP. GRADE : Exd IIB T4	D.P(S/U) : F.V-0.3Mpa / 0.3Mpa
D.T(S/U) : -70~150℃ / -70~150℃		D.T(S/U) : -40~150℃ / -40~150℃

NOTE : 원심분리기 EGR-301 공동사용

△	주후 리비전 기록	리비전기	참조	2019.09.04	J.H LEE	J.H LEE	J.H LEE
△	배관 변경			2019.06.03	S.G LEE	J.J JIEONG	Y.J KIM
△	배관 변경			2019.05.13	S.G LEE	J.J JIEONG	Y.J KIM
△	REVISION			2019.04.18	S.G LEE	J.J JIEONG	Y.J KIM
△	REVISION			2019.02.21	S.G LEE	J.J JIEONG	Y.J KIM
△	for APPROVAL			2019.01.24	S.G LEE	J.J JIEONG	Y.J KIM
REV.	REVISIONS	DATE	DRAWN	CHK'D	APP'D		
PROJECT NAME 공주공장 합성, 정제 증축공사							
CLIENT (주)이지캠							
PREPARED BY CT CT ENG Co.,Ltd.							
PROJECTION	TITLE P & ID (4/8-EGR301) HAC REACTION SYSTEM						
SCALE N.S	DATE 2018.11.14	DWG. NO EGC-PID-181101-304				REV.	