


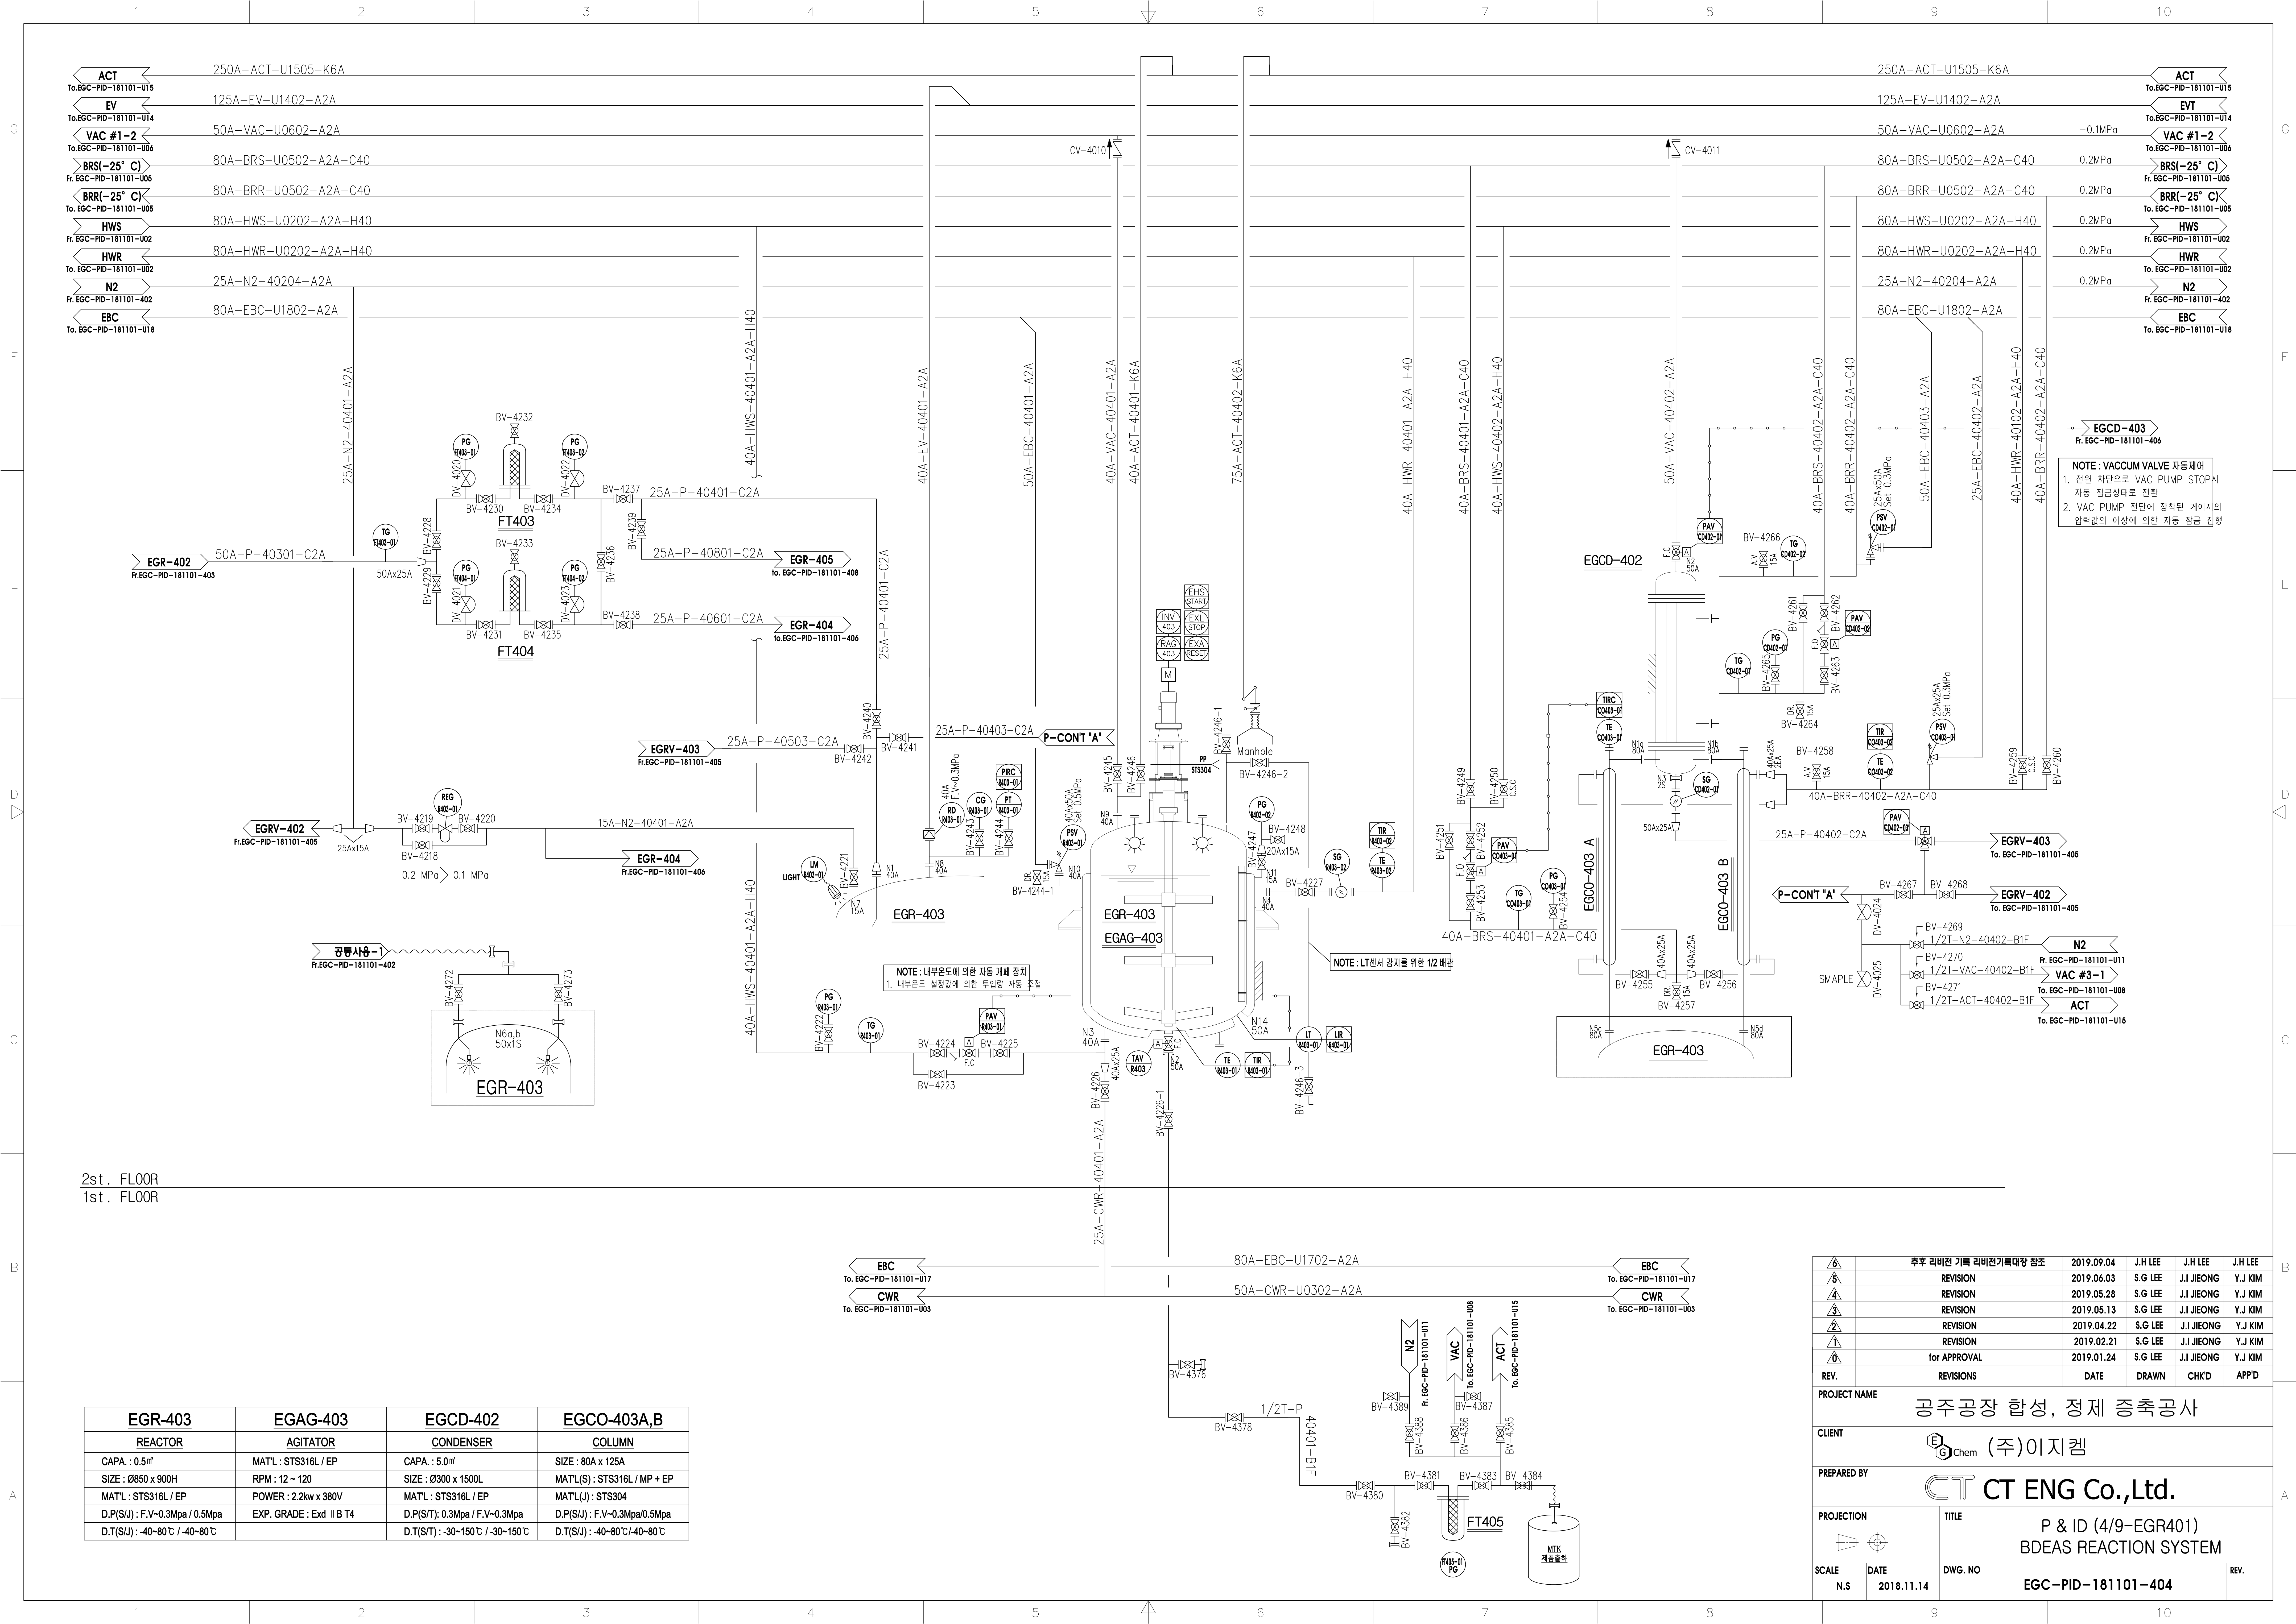

EGR-403	EGAG-403	EGCD-402	EGCO-403A,B
REACTOR	AGITATOR	CONDENSER	COLUMN
CAPA : 0.5㎡	MAT'L : STS316L / EP	CAPA : 5.0㎡	SIZE : 80A x 125A
SIZE : Ø850 x 900H	RPM : 12 ~ 120	SIZE : Ø300 x 1500L	MAT'L(S) : STS316L / MP + EP
MAT'L : STS316L / EP	POWER : 2.2kw x 380V	MAT'L : STS316L / EP	MAT'L(U) : STS304
D.P(S/U) : F.V-0.3Mpa / 0.5Mpa	EXP. GRADE : Exd II B T4	D.P(S/T) : 0.3Mpa / F.V-0.3Mpa	D.P(S/U) : F.V-0.3Mpa/0.5Mpa
D.T(S/U) : -40~80℃ / -40~80℃		D.T(S/T) : -30~150℃ / -30~150℃	D.T(S/U) : -40~80℃/-40~80℃

△	후후 리버전 기록 리버전기록대장 참조	2019.09.04	J.H LEE	J.H LEE	J.H LEE
△	REVISION	2019.06.03	S.G LEE	J.I JEONG	Y.J KIM
△	REVISION	2019.05.28	S.G LEE	J.I JEONG	Y.J KIM
△	REVISION	2019.05.13	S.G LEE	J.I JEONG	Y.J KIM
△	REVISION	2019.04.22	S.G LEE	J.I JEONG	Y.J KIM
△	REVISION	2019.02.21	S.G LEE	J.I JEONG	Y.J KIM
△	for APPROVAL	2019.01.24	S.G LEE	J.I JEONG	Y.J KIM
REV.	REVISIONS	DATE	DRAWN	CHK'D	APP'D
PROJECT NAME 공주공장 합성, 정제 증축공사					
CLIENT (주)이지캠					
PREPARED BY CT CT ENG Co.,Ltd.					
PROJECTION	TITLE P & ID (4/9-EGR401) BDEAS REACTION SYSTEM				
SCALE N.S	DATE 2018.11.14	DWG. NO EGC-PID-181101-404	REV.		