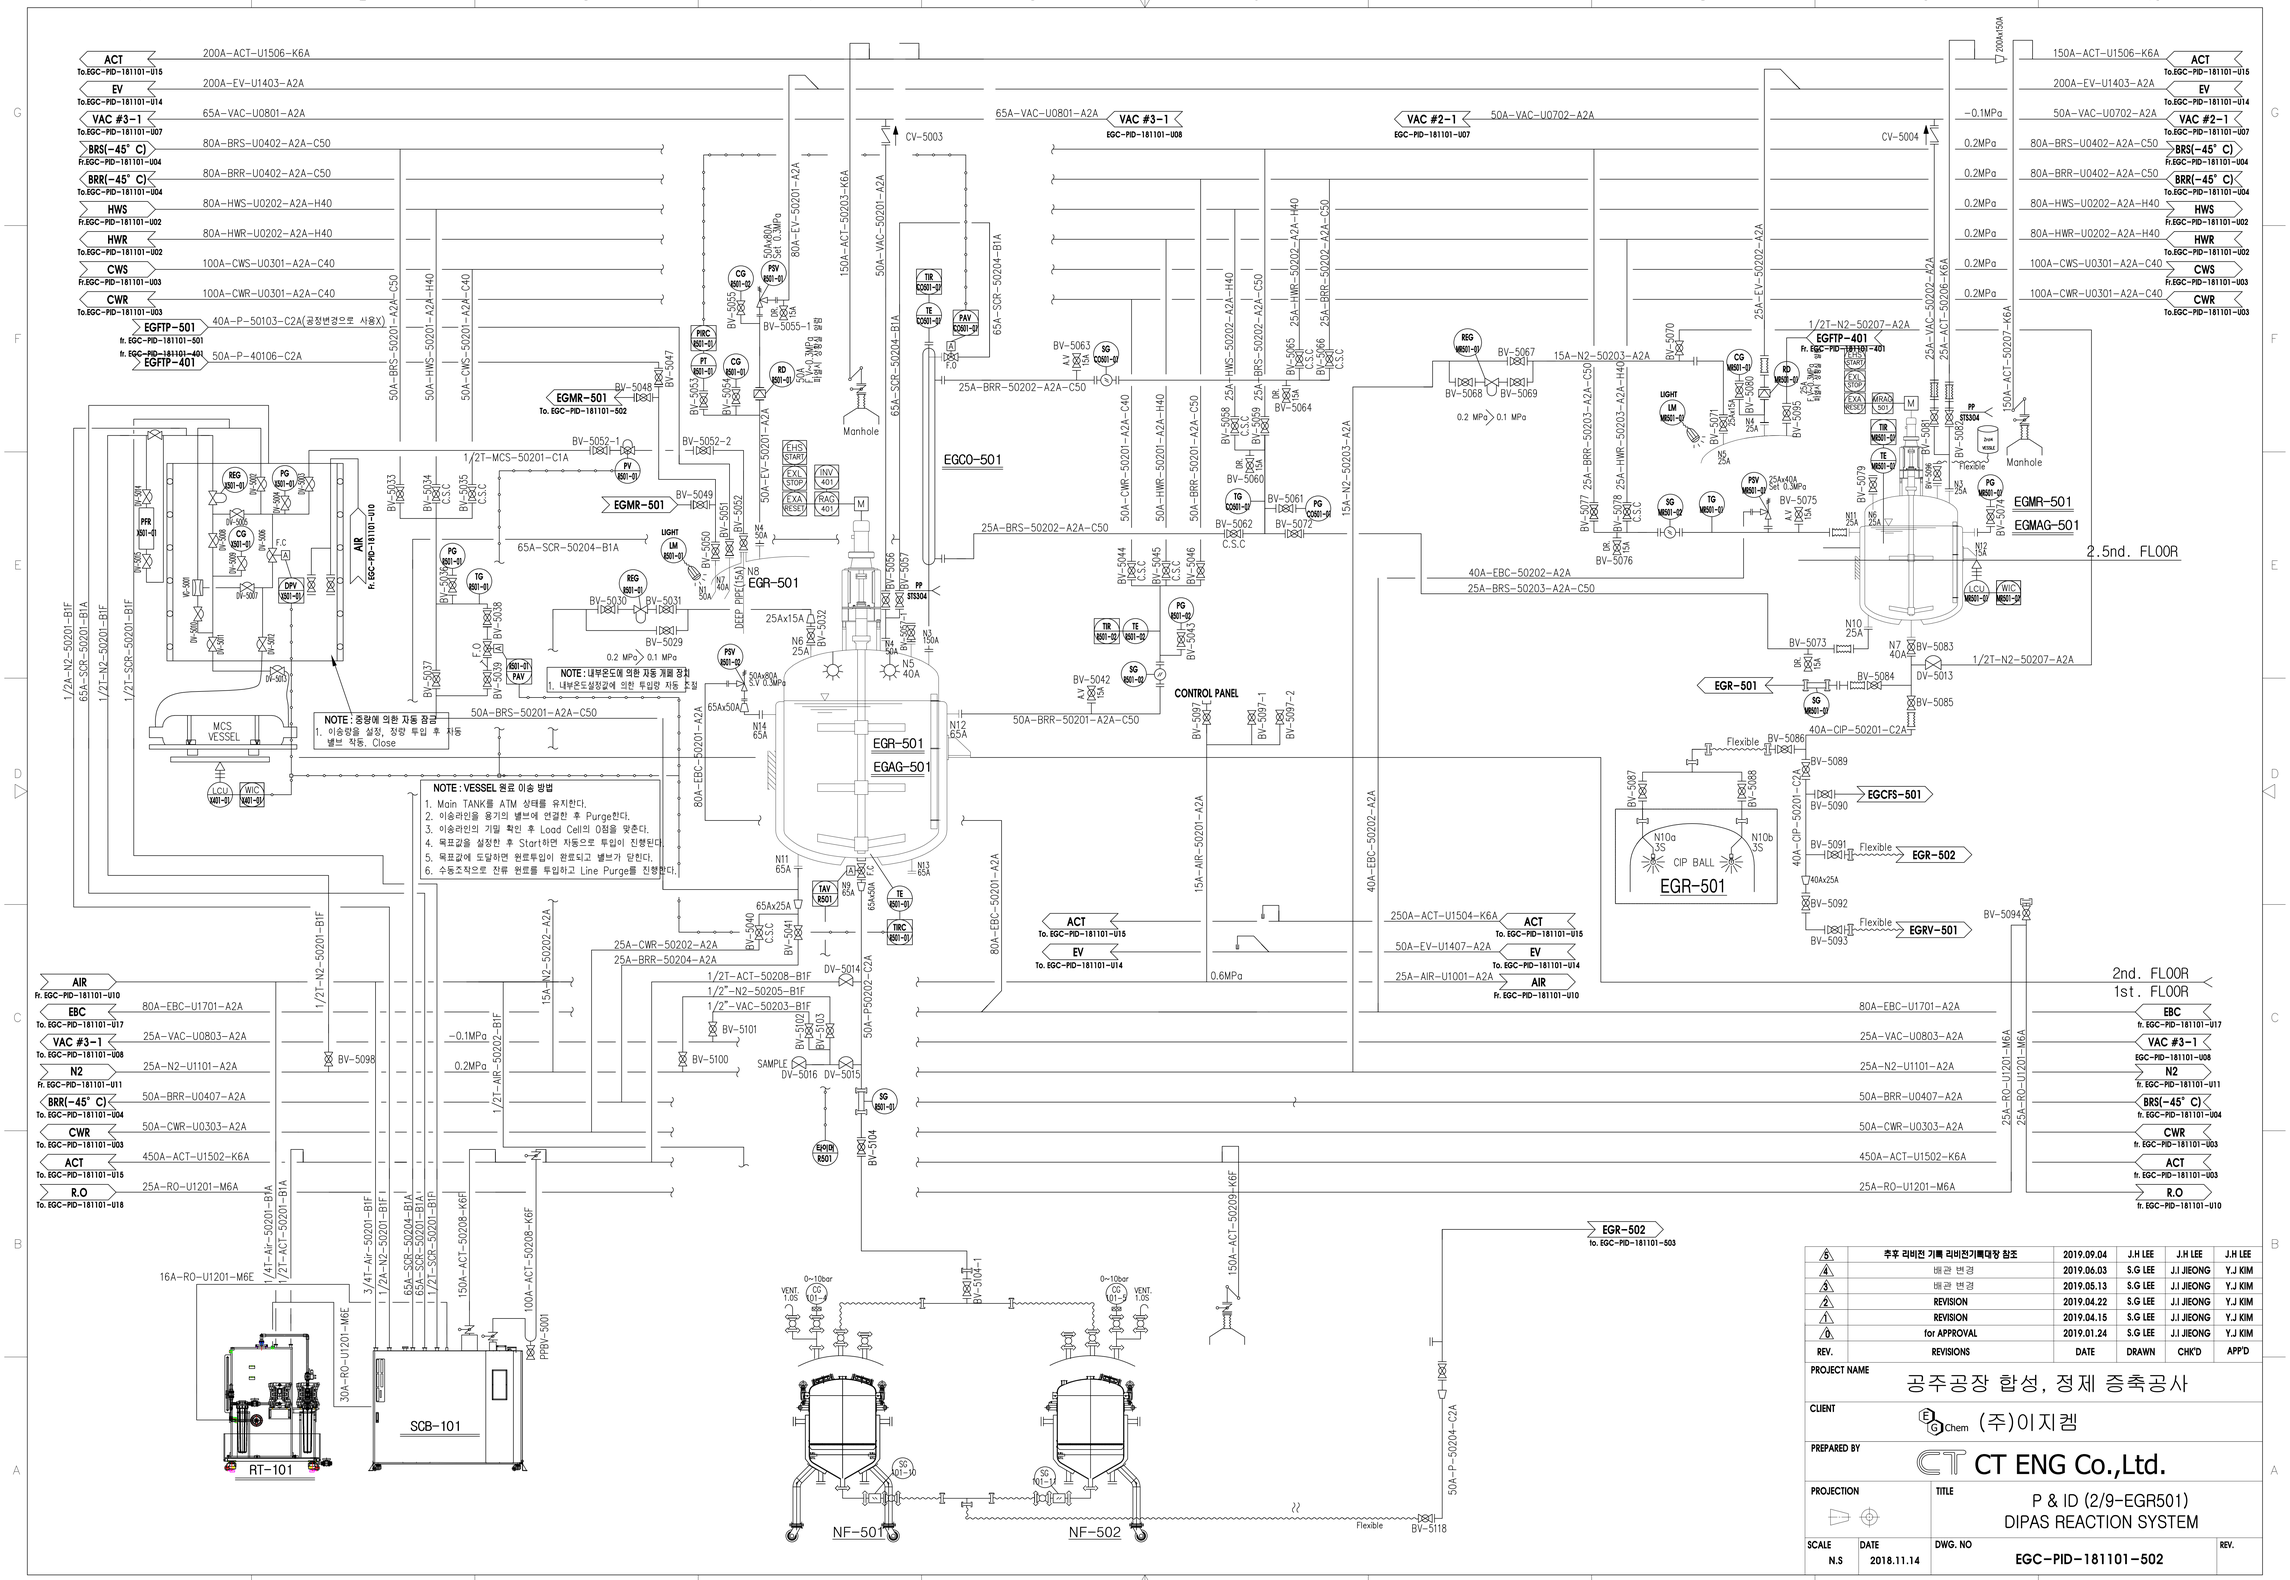

5	추후 리비전 기록 리비전기록대장 참조	2019.09.04	J.H LEE	J.H LEE	J.H LEE
4	배관 변경	2019.06.03	S.G LEE	J.I JIEONG	Y.J KIM
3	배관 변경	2019.05.13	S.G LEE	J.I JIEONG	Y.J KIM
2	REVISION	2019.04.22	S.G LEE	J.I JIEONG	Y.J KIM
1	REVISION	2019.04.15	S.G LEE	J.I JIEONG	Y.J KIM
0	for APPROVAL	2019.01.24	S.G LEE	J.I JIEONG	Y.J KIM
REV.	REVISIONS	DATE	DRAWN	CHK'D	APP'D

PROJECT NAME: 공주공장 합성, 정제 증축공사

CLIENT: EGChem (주)이지켐

PREPARED BY: CT ENG Co.,Ltd.

PROJECTION

TITLE: P & ID (2/9-EGR501) DIPAS REACTION SYSTEM

SCALE	DATE	DWG. NO	REV.
N.S	2018.11.14	EGC-PID-181101-502	

EFCFTP-501	EGCO-501	SCB-101	RT-101	NF-501, 502	EGR-501	EGAG-501	EGMR-501	EGMAG-501
MAGNETIC TRASFER PUMP	COLUMN	SCRUBBER	Recirculation Tank	Nutsche Filter	REACTOR	AGITATOR	REACTOR	AGITATOR
CAPA. : 0.12㎥/min x 20mH	SIZE : 150A x 200A	CAPA : STS316L / MP + EP	SIZE : 985(W)x800(D)x1342(H)	CAPA : 1200 Liter	CAPA. : 3.0㎥	MAT'L : STS316L / EP	CAPA. : 0.3㎥	MAT'L : STS316L / EP
MAT'L : STS316L	MAT'L(S) : STS316L / MP + EP	TYPE : HEAT&WET	System material : PVC	MAT'L : STS316L	SIZE : Ø1500 x 1800H	RPM : 12 ~ 90 (1/20)	SIZE : Ø700 x 800H	RPM : 20 ~ 117 (1/15)
POWER : 1.5kw x 2P x 380V	MAT'L(J) : STS304	SIZE : 1,100 ×1,350 ×2,000	INLET / OUTLET: 16A PVC	POWER : N/A	MAT'L : STS316L / EP	POWER : 7.5kw x 380V x 4pole	MAT'L : STS316L / EP	POWER : 2.2kw x 380V x 4pole
EXP. GRADE : Exd ⅡB T4	D.P(S/J) : F.V~0.3Mpa / 0.3Mpa	Heating temperature : 700~750℃	INLET / OUTLET: 16A PVC	D.P(S/J) : FV~0.18 MPA.	D.P(S/J) : F.V~0.3Mpa / 0.3Mpa	EXP. GRADE : Exd ⅡB T4	D.P(S/J) : F.V~0.2Mpa / 0.25Mpa	EXP. GRADE : Exd ⅡB T4
	D.T(S/J) : -40~150℃ / -40~150℃			D.T(S/J) : -30~150 ° C	D.T(S/J) : -70~150℃ / -70~150℃		D.T(S/J) : -20~80℃ / -20~80℃	