


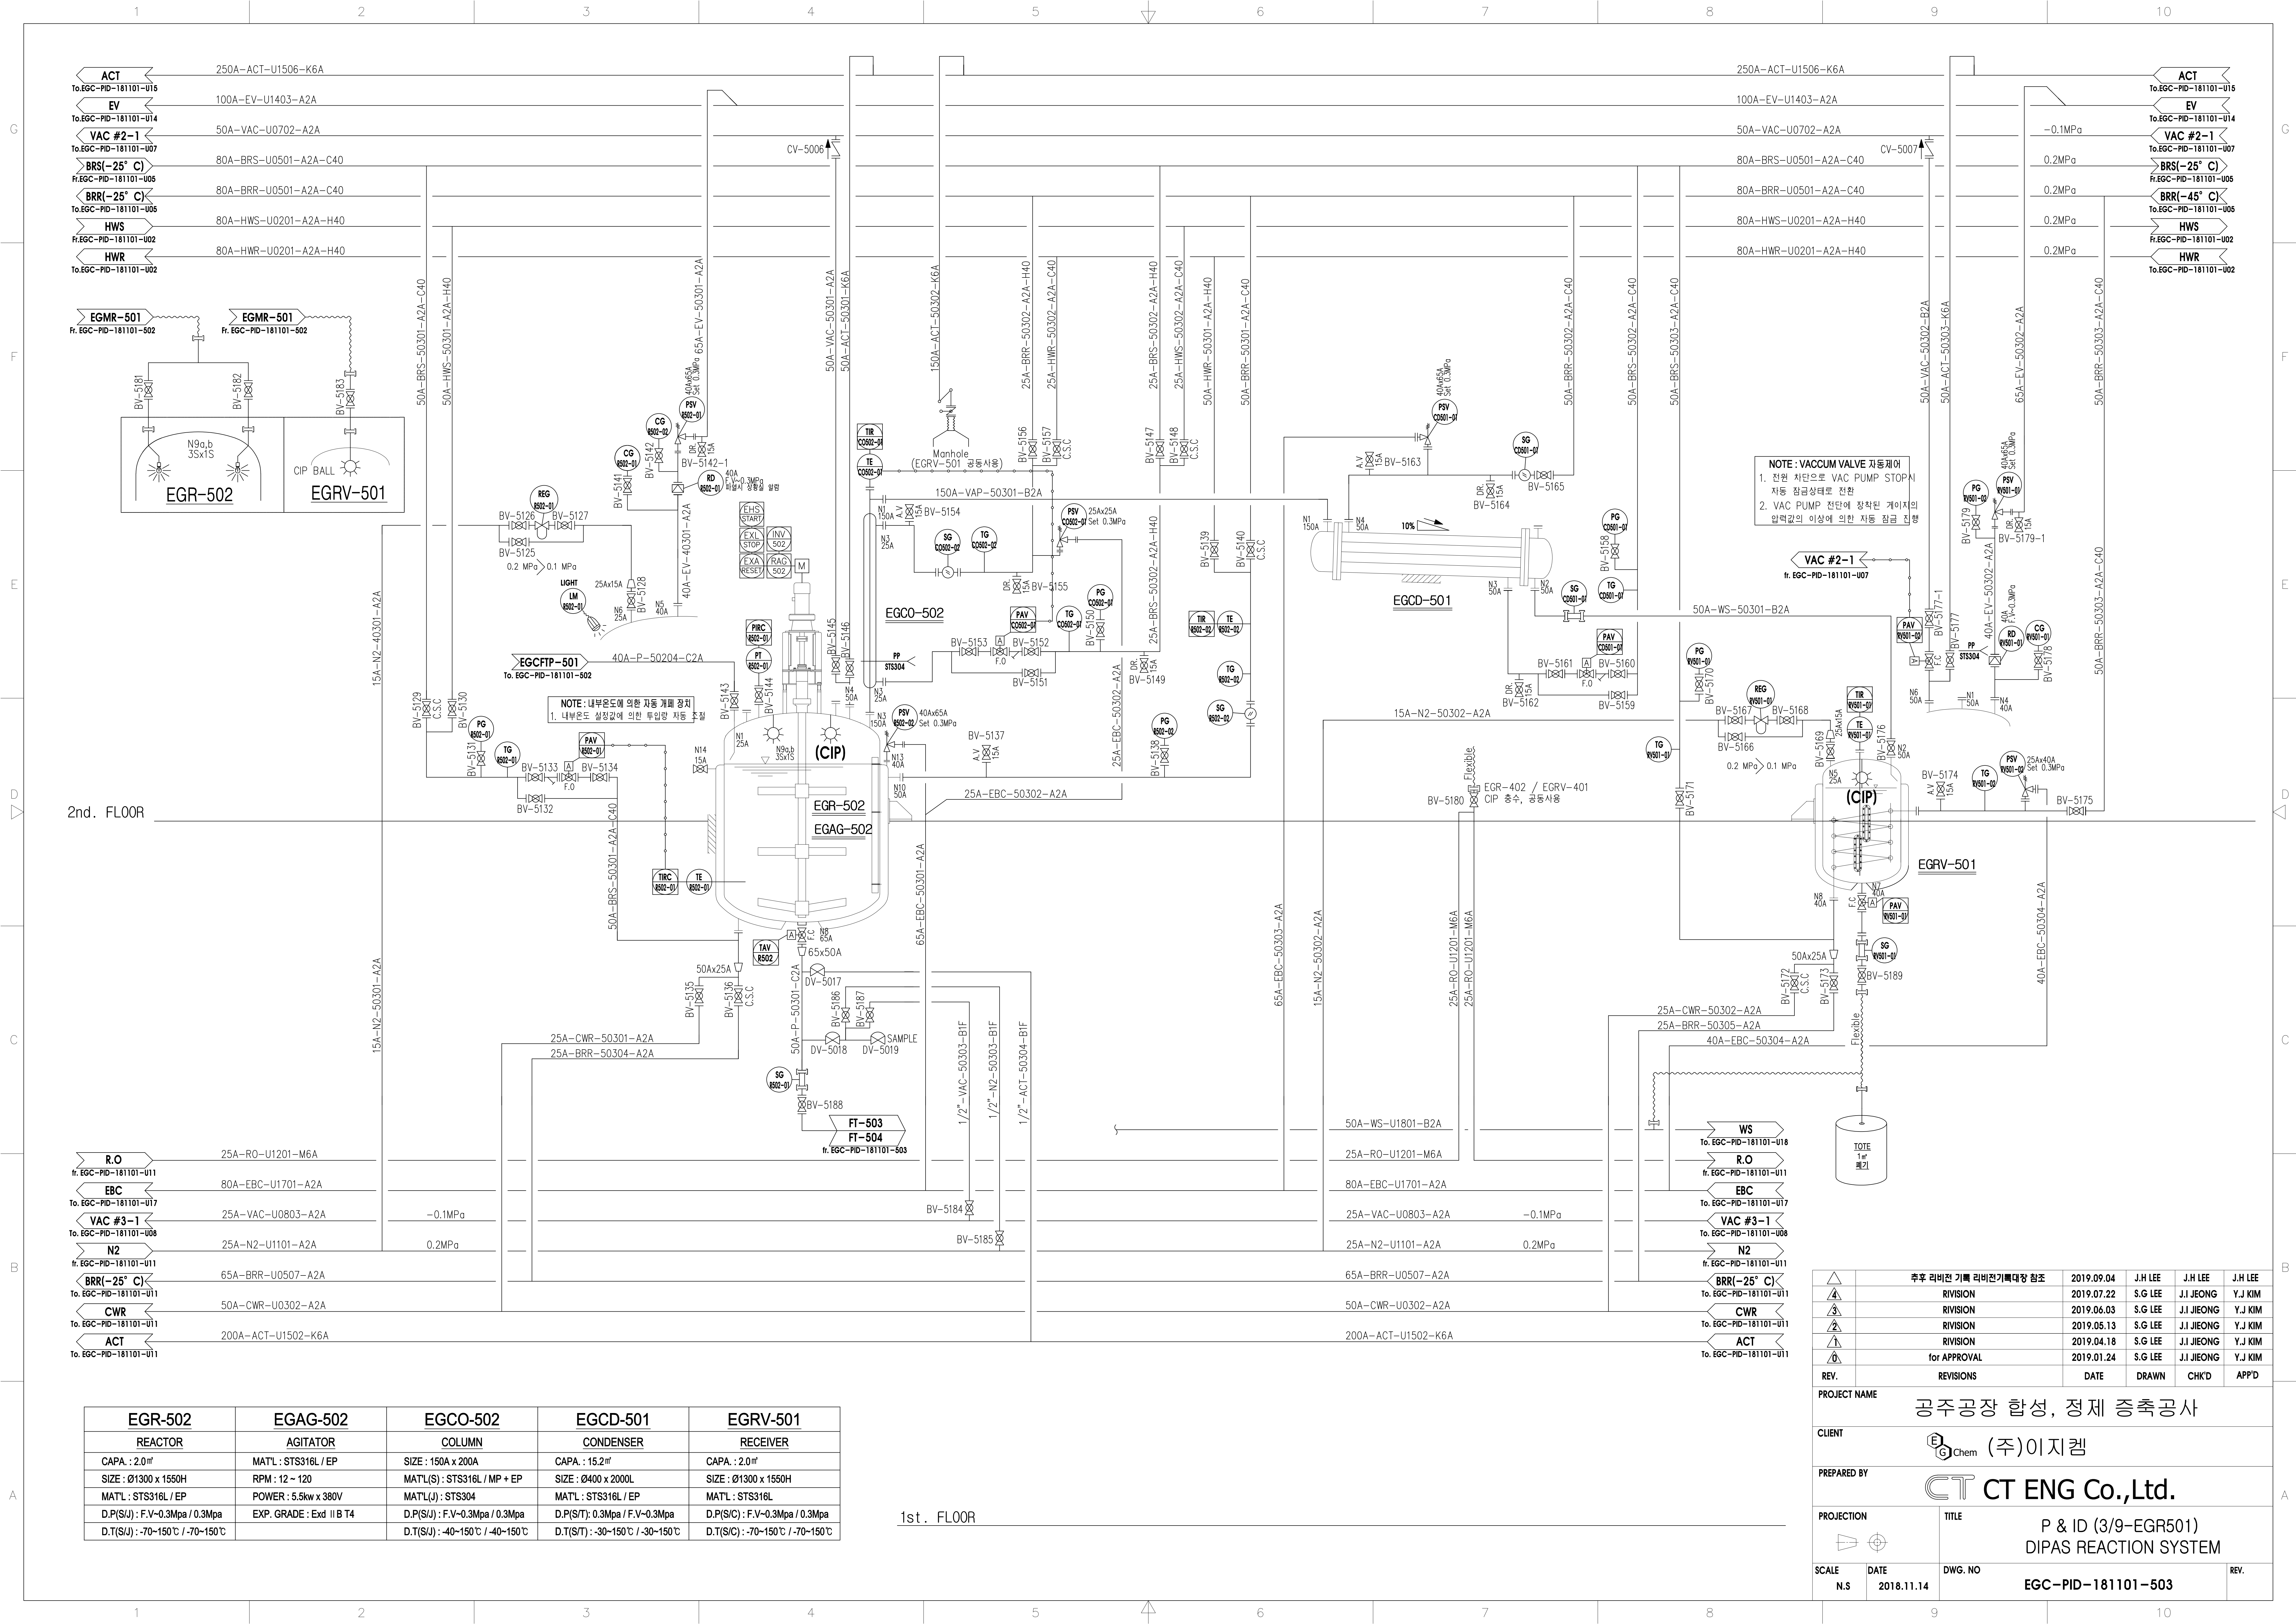

EGR-502	EGAG-502	EGO-502	EGCD-501	EGRV-501
REACTOR	AGITATOR	COLUMN	CONDENSER	RECEIVER
CAPA : 2.0㎡	MATL : STS316L / EP	SIZE : 150A x 200A	CAPA : 15.2㎡	CAPA : 2.0㎡
SIZE : Ø1300 x 1550H	RPM : 12 ~ 120	MATL(S) : STS316L / MP + EP	SIZE : Ø400 x 2000L	SIZE : Ø1300 x 1550H
MATL : STS316L / EP	POWER : 5.5kw x 380V	MATL(J) : STS304	MATL : STS316L / EP	MATL : STS316L
D.P(S/U) : F.V-0.3Mpa / 0.3Mpa	EXP. GRADE : Exd II B T4	D.P(S/U) : F.V-0.3Mpa / 0.3Mpa	D.P(S/T) : 0.3Mpa / F.V-0.3Mpa	D.P(S/C) : F.V-0.3Mpa / 0.3Mpa
D.T(S/U) : -70~150℃ / -70~150℃		D.T(S/U) : -40~150℃ / -40~150℃	D.T(S/T) : -30~150℃ / -30~150℃	D.T(S/C) : -70~150℃ / -70~150℃

△	주요 리비전 기록 리비전기대장 참조	2019.09.04	J.H LEE	J.H LEE	J.H LEE
④	RIVISION	2019.07.22	S.G LEE	J.I JEONG	Y.J KIM
③	RIVISION	2019.06.03	S.G LEE	J.I JEONG	Y.J KIM
②	RIVISION	2019.05.13	S.G LEE	J.I JEONG	Y.J KIM
①	RIVISION	2019.04.18	S.G LEE	J.I JEONG	Y.J KIM
①	for APPROVAL	2019.01.24	S.G LEE	J.I JEONG	Y.J KIM
REV.	REVISIONS	DATE	DRAWN	CHK'D	APP'D
PROJECT NAME 공주공장 합성, 정제 증축공사					
CLIENT (주)이지캠					
PREPARED BY CT ENG Co.,Ltd.					
PROJECTION		TITLE P & ID (3/9-EGR501) DIPAS REACTION SYSTEM			
SCALE N.S	DATE 2018.11.14	DWG. NO EGC-PID-181101-503	REV.		