


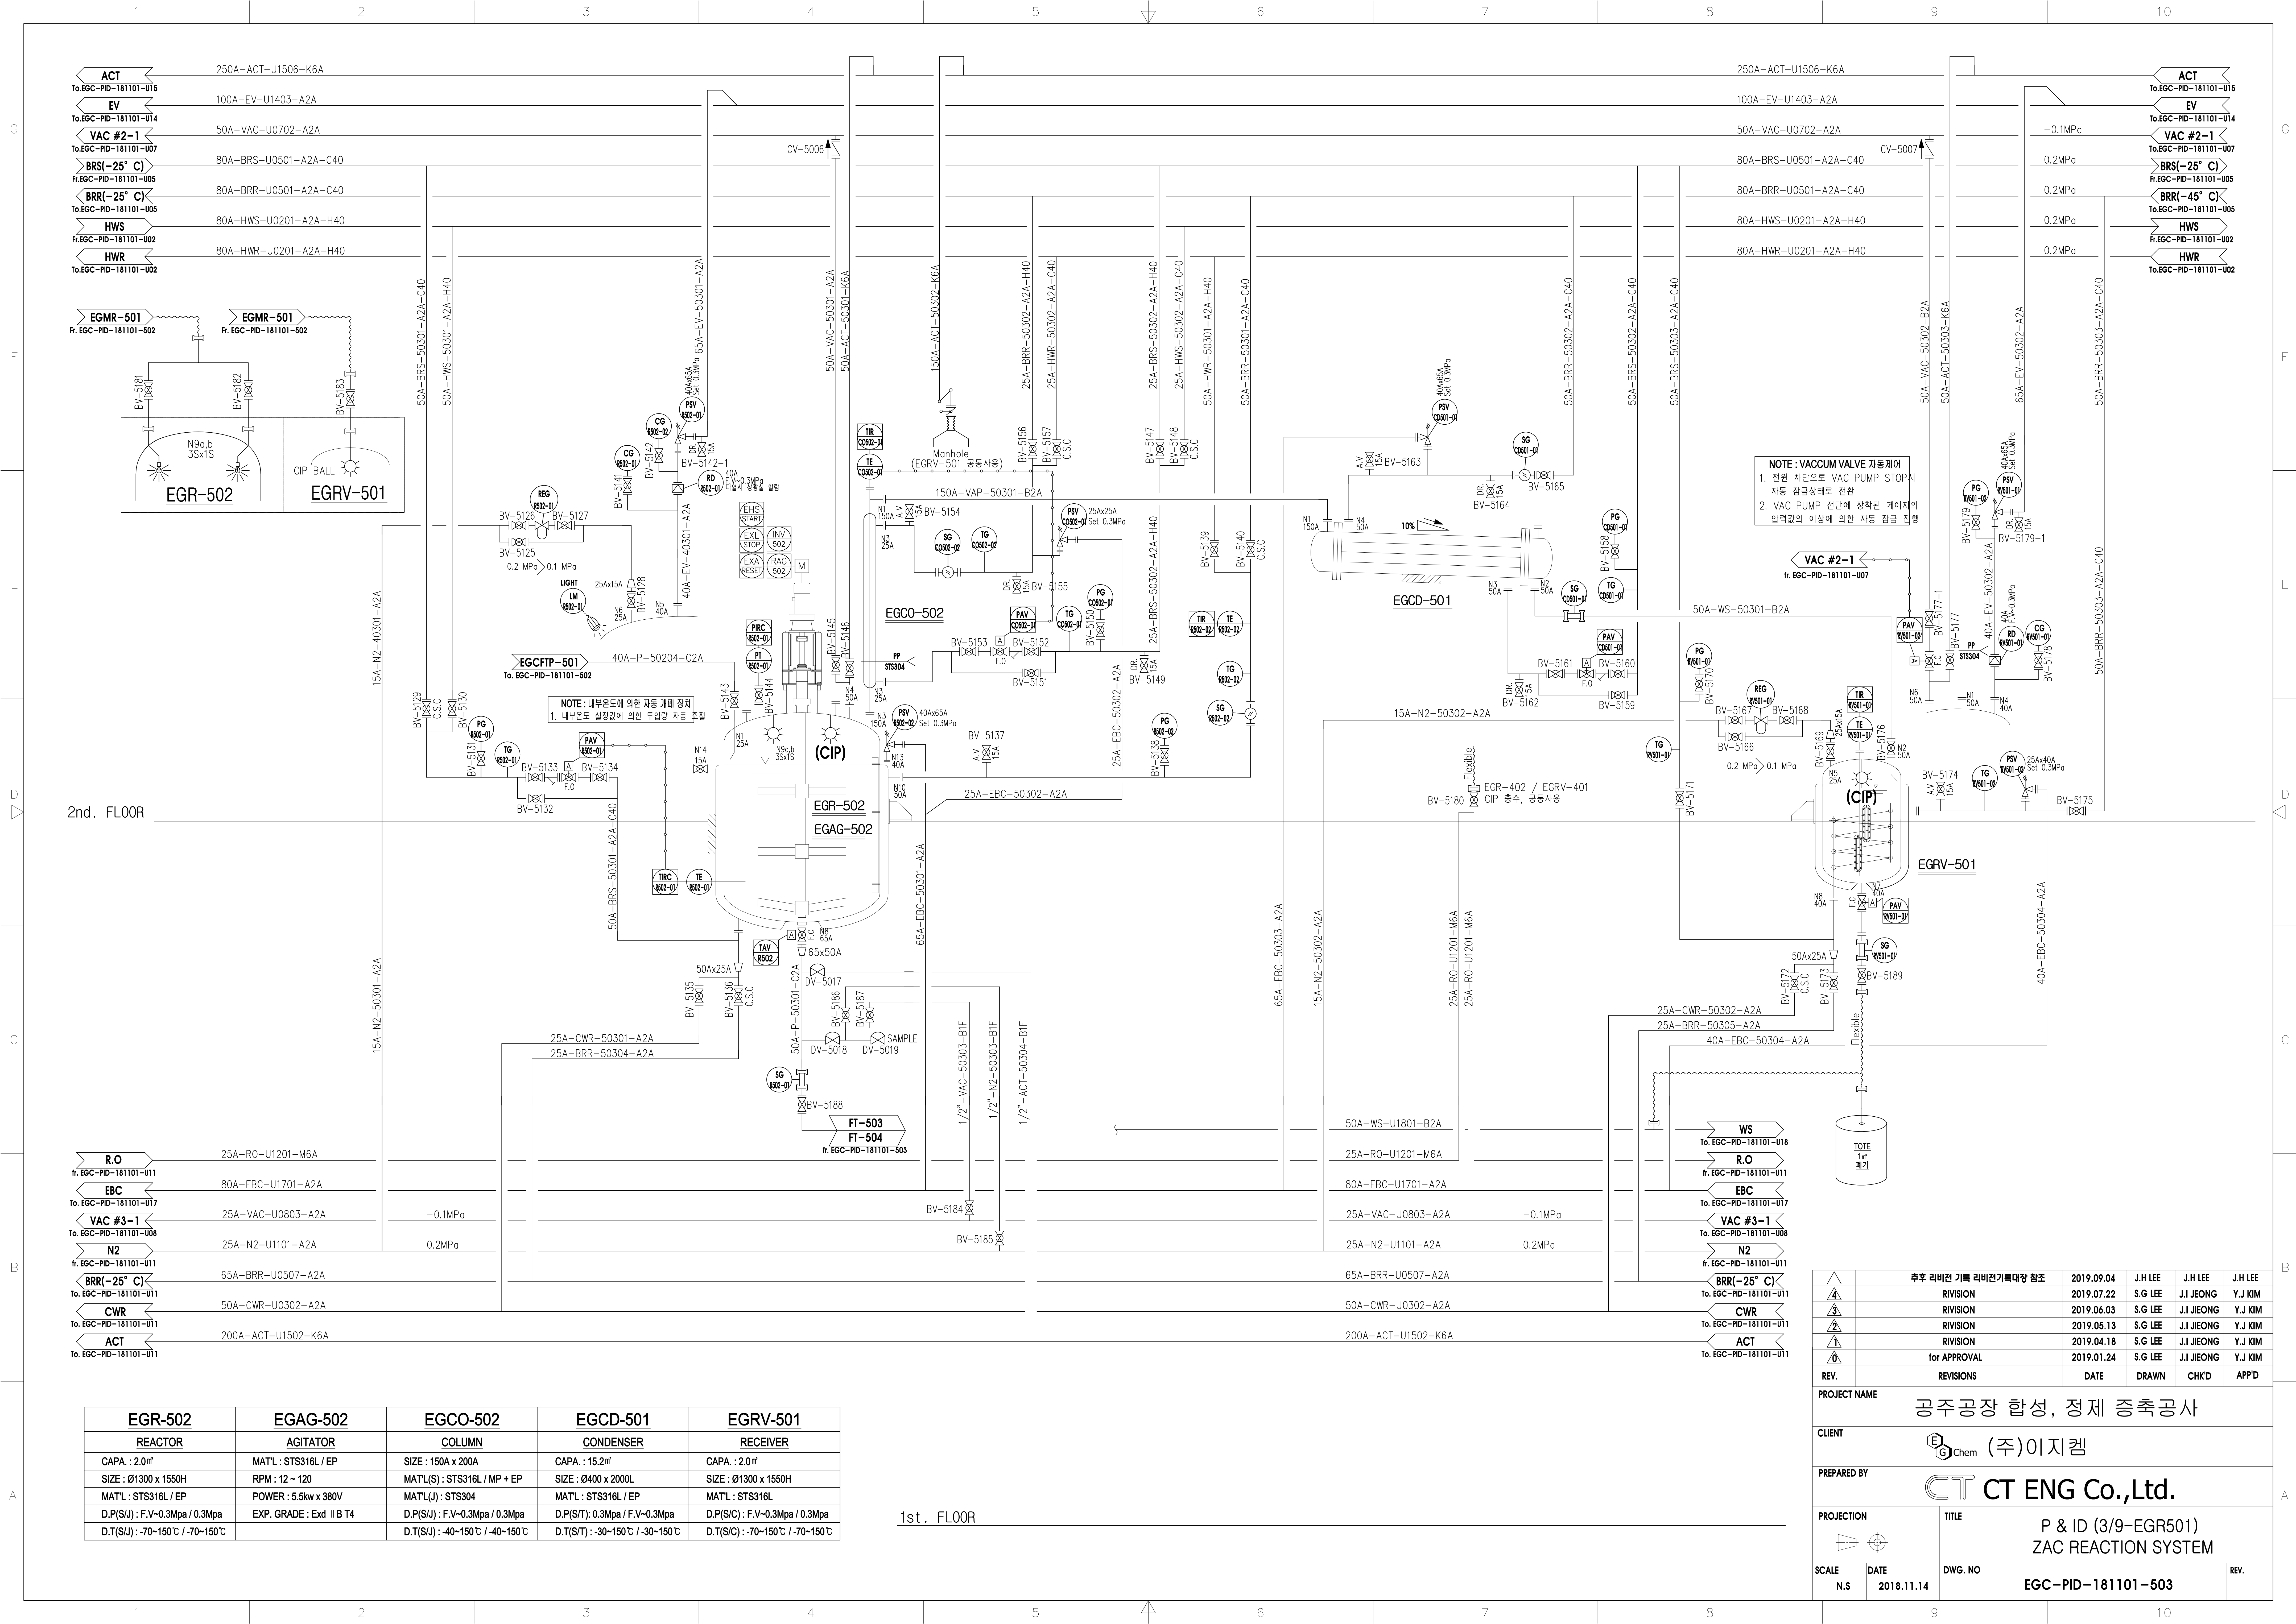

| EGR-502                        | EGAG-502                 | EGO-502                        | EGCD-501                       | EGRV-501                       |
|--------------------------------|--------------------------|--------------------------------|--------------------------------|--------------------------------|
| REACTOR                        | AGITATOR                 | COLUMN                         | CONDENSER                      | RECEIVER                       |
| CAPA : 2.0m <sup>3</sup>       | MATL : STS316L / EP      | SIZE : 150A x 200A             | CAPA : 15.2m <sup>3</sup>      | CAPA : 2.0m <sup>3</sup>       |
| SIZE : Ø1300 x 1550H           | RPM : 12 ~ 120           | MATL(S) : STS316L / MP + EP    | SIZE : Ø400 x 2000L            | SIZE : Ø1300 x 1550H           |
| MATL : STS316L / EP            | POWER : 5.5kw x 380V     | MATL(J) : STS304               | MATL : STS316L / EP            | MATL : STS316L                 |
| D.P(S/U) : F.V-0.3Mpa / 0.3Mpa | EXP. GRADE : Exd II B T4 | D.P(S/U) : F.V-0.3Mpa / 0.3Mpa | D.P(S/T) : 0.3Mpa / F.V-0.3Mpa | D.P(S/C) : F.V-0.3Mpa / 0.3Mpa |
| D.T(S/U) : -70~150℃ / -70~150℃ |                          | D.T(S/U) : -40~150℃ / -40~150℃ | D.T(S/T) : -30~150℃ / -30~150℃ | D.T(S/C) : -70~150℃ / -70~150℃ |

|                               |                                               |                            |         |           |         |
|-------------------------------|-----------------------------------------------|----------------------------|---------|-----------|---------|
| △                             | 주요 리비전 기록 리비전기대장 참조                           | 2019.09.04                 | J.H LEE | J.H LEE   | J.H LEE |
| ④                             | RIVISION                                      | 2019.07.22                 | S.G LEE | J.I JEONG | Y.J KIM |
| ③                             | RIVISION                                      | 2019.06.03                 | S.G LEE | J.I JEONG | Y.J KIM |
| ②                             | RIVISION                                      | 2019.05.13                 | S.G LEE | J.I JEONG | Y.J KIM |
| ①                             | RIVISION                                      | 2019.04.18                 | S.G LEE | J.I JEONG | Y.J KIM |
| ①                             | for APPROVAL                                  | 2019.01.24                 | S.G LEE | J.I JEONG | Y.J KIM |
| REV.                          | REVISIONS                                     | DATE                       | DRAWN   | CHK'D     | APP'D   |
| PROJECT NAME 공주공장 합성, 정제 증축공사 |                                               |                            |         |           |         |
| CLIENT  (주)이지캠                |                                               |                            |         |           |         |
| PREPARED BY  CT ENG Co.,Ltd.  |                                               |                            |         |           |         |
| PROJECTION                    | TITLE P & ID (3/9-EGR501) ZAC REACTION SYSTEM |                            |         |           |         |
| SCALE N.S                     | DATE 2018.11.14                               | DWG. NO EGC-PID-181101-503 |         | REV.      |         |