


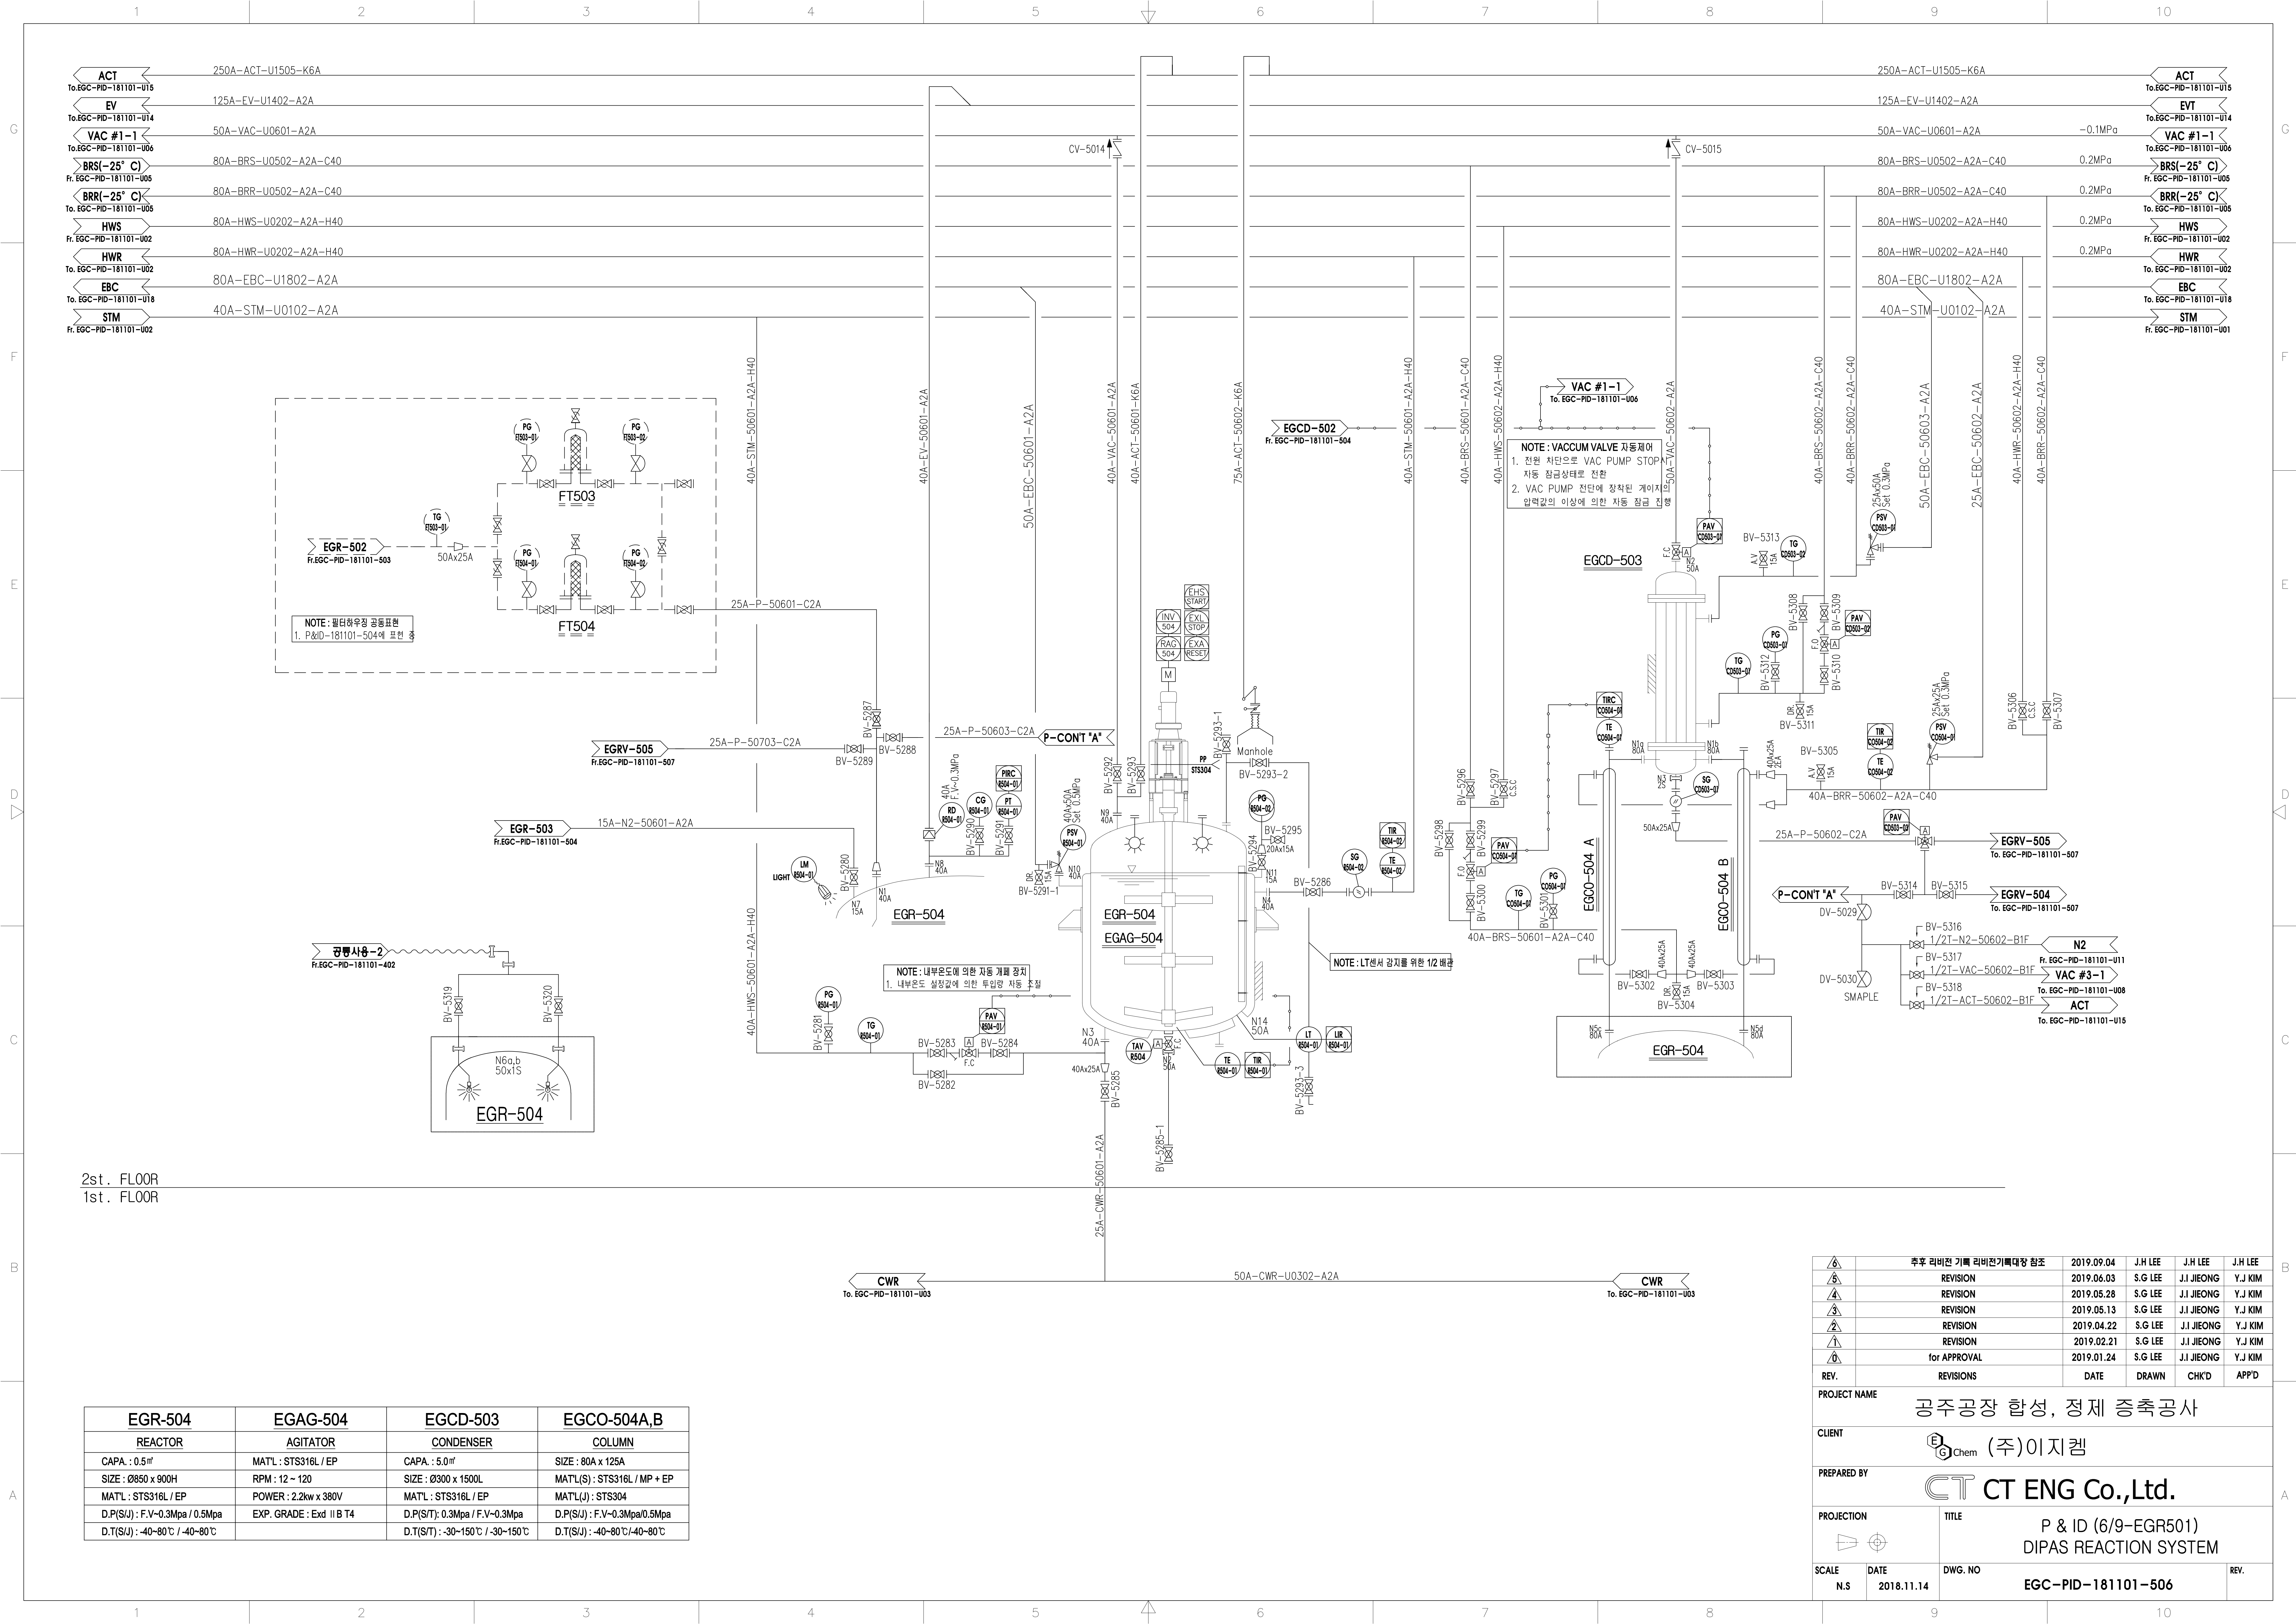

EGR-504	EGAG-504	EGCD-503	EGCO-504A,B
REACTOR	AGITATOR	CONDENSER	COLUMN
CAPA : 0.5㎡	MAT'L : STS316L / EP	CAPA : 5.0㎡	SIZE : 80A x 125A
SIZE : Ø850 x 900H	RPM : 12 ~ 120	SIZE : Ø300 x 1500L	MAT'L(S) : STS316L / MP + EP
MAT'L : STS316L / EP	POWER : 2.2kw x 380V	MAT'L : STS316L / EP	MAT'L(U) : STS304
D.P(S/U) : F.V-0.3Mpa / 0.5Mpa	EXP. GRADE : Exd II B T4	D.P(S/T) : 0.3Mpa / F.V-0.3Mpa	D.P(S/U) : F.V-0.3Mpa/0.5Mpa
D.T(S/U) : -40~80℃ / -40~80℃		D.T(S/T) : -30~150℃ / -30~150℃	D.T(S/U) : -40~80℃ / -40~80℃

△	후후 리버전 기록 리버전기록대장 참조	2019.09.04	J.H LEE	J.H LEE	J.H LEE
△	REVISION	2019.06.03	S.G LEE	J.I JIEONG	Y.J KIM
△	REVISION	2019.05.28	S.G LEE	J.I JIEONG	Y.J KIM
△	REVISION	2019.05.13	S.G LEE	J.I JIEONG	Y.J KIM
△	REVISION	2019.04.22	S.G LEE	J.I JIEONG	Y.J KIM
△	REVISION	2019.02.21	S.G LEE	J.I JIEONG	Y.J KIM
△	for APPROVAL	2019.01.24	S.G LEE	J.I JIEONG	Y.J KIM
REV.	REVISIONS	DATE	DRAWN	CHK'D	APP'D
PROJECT NAME 공주공장 합성, 정제 증축공사					
CLIENT (주)이지캠					
PREPARED BY CT ENG Co.,Ltd.					
PROJECTION	TITLE P & ID (6/9-EGR501) DIPAS REACTION SYSTEM				
SCALE N.S	DATE 2018.11.14	DWG. NO EGC-PID-181101-506	REV.		